



全体一般図 (その1)

側面図 S=1:300

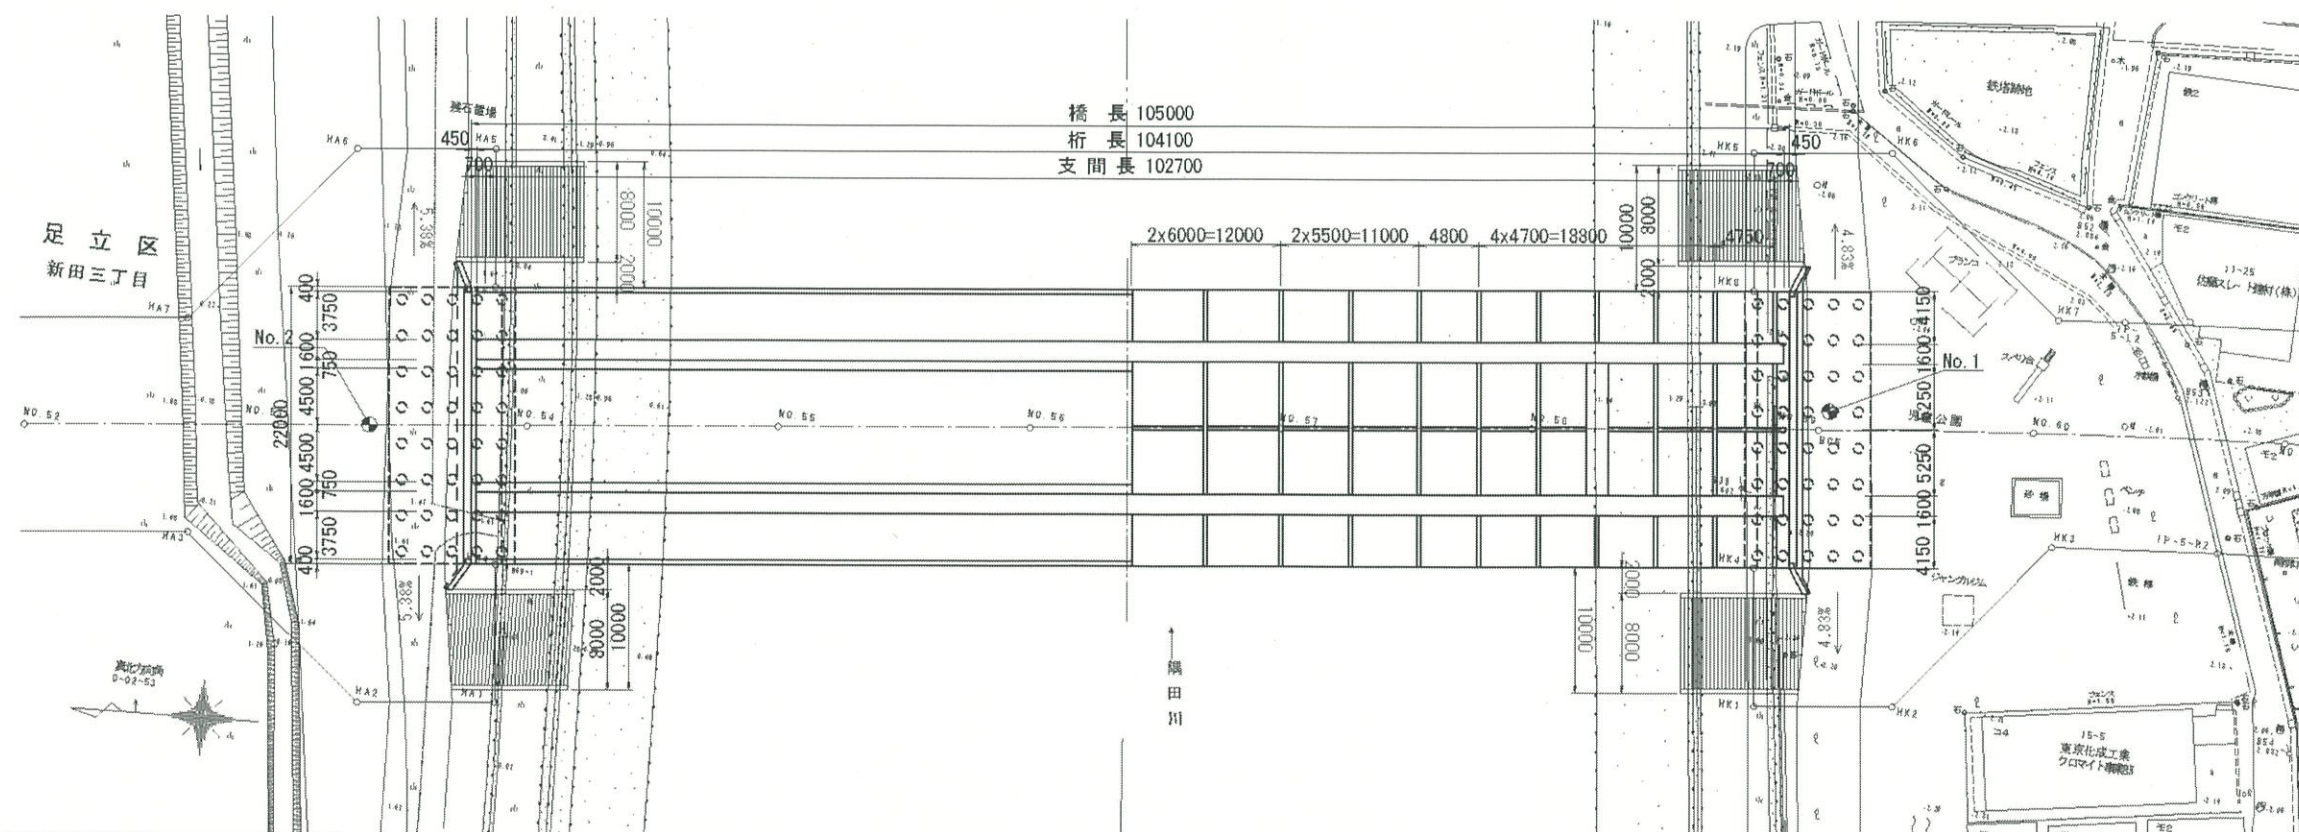

日付

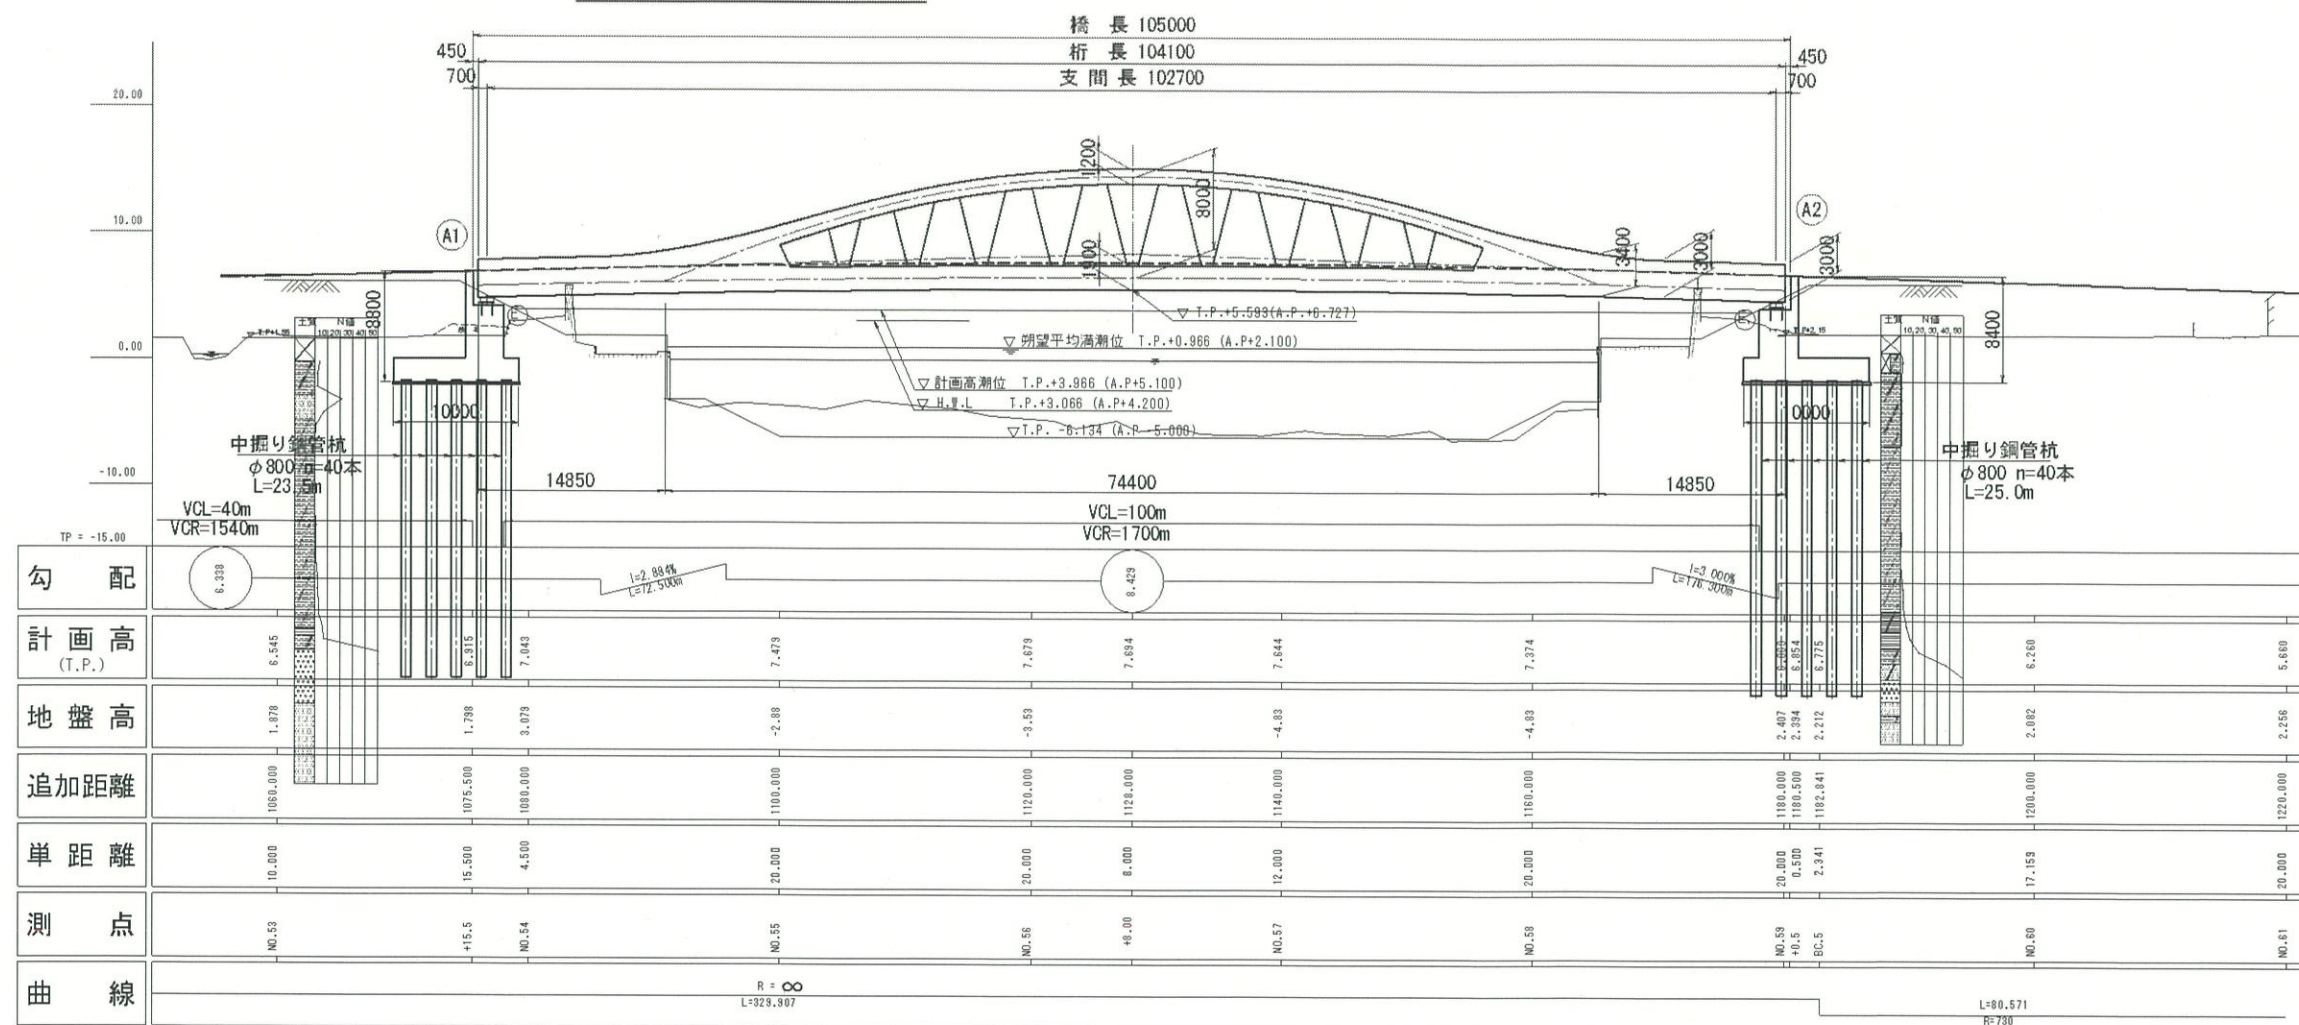

都市機構 東京都心支社

部長

次長

チームリーダー

担当

設計事務所

大日本コンサルタント (株)

工事名称

新田三丁目地区開発新田豊島橋 (仮称)
上郷工建設工事 (第1回変更)

設計名称

新田豊島橋 (仮称) 実施設計

図面名称

全体一般図 (その1)

縮尺

図示

図面番号

J-3