



アーチリブ (その1-1) S=1:30


配置図 S=1:300

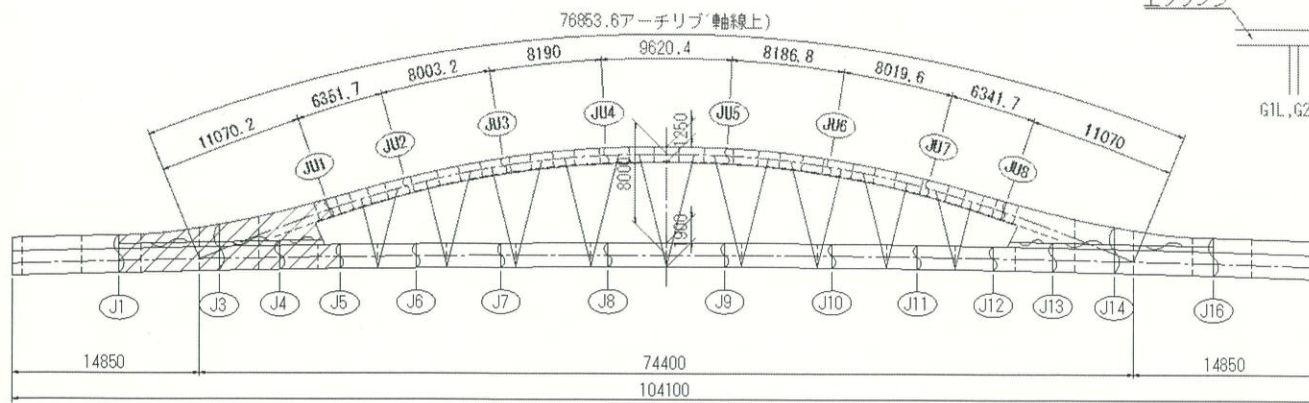


面取り処理図 S=1:10

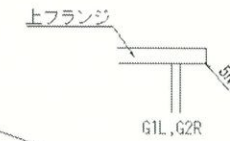


E-E

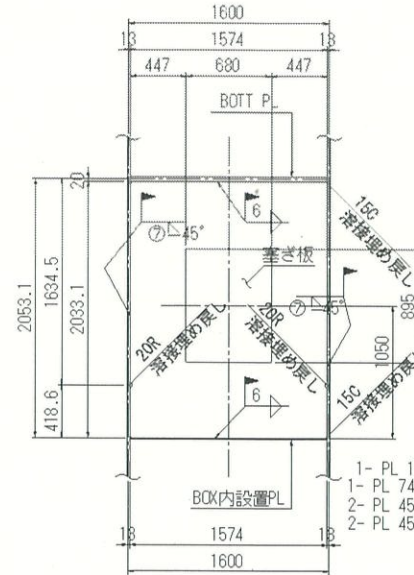


補助照明取付詳細 S=1:10

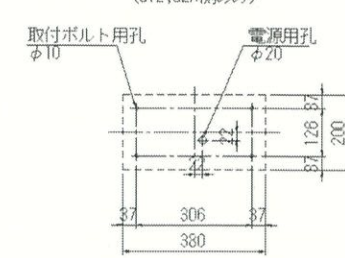


b-b

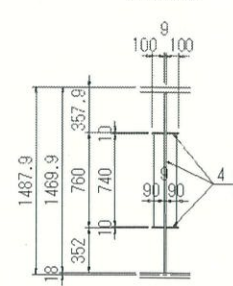


"A"部詳細 S=1:10

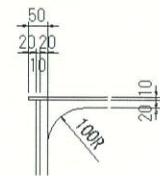


D1

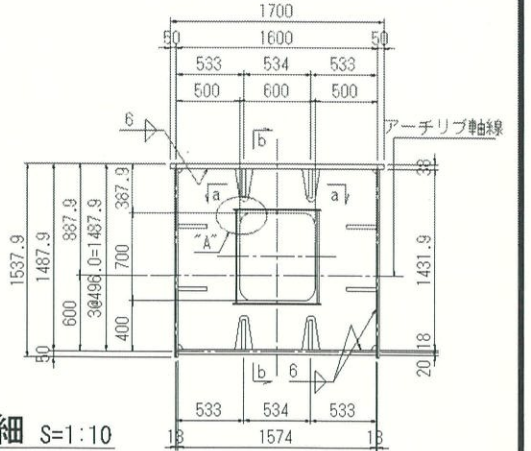


a-a

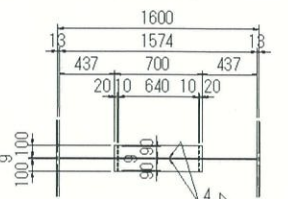

C-C


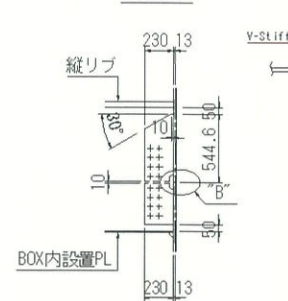


吊り金具詳細 S=1:10

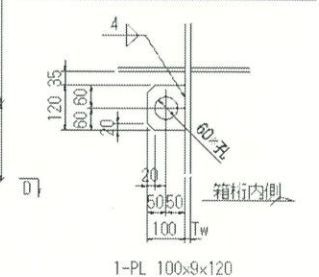

- ① 2-WEB PL 1293x23x7982 (SM570TMC)
- ② 2-WEB PL 3151x23x9044 (SM570TMC)
- ③ 2-WEB PL 2289x23x8003 (SM570TMC)
- ④ 2-WEB PL 2290x23x4894 (SM570TMC)
- ⑤ 2-WEB PL 2291x23x4783 (SM570TMC)
- ⑥ 2-RIB PL 190x19x1596 (SM490YB)
- ⑦ 2-RIB PL 190x19x3612 (SM490YB)
- ⑧ 4-RIB PL 190x19x706 (SM490YB)
- ⑨ 2-RIB PL 230x25x561 (SM570TMC)
- ⑩ 2-RIB PL 230x25x1180 (SM570TMC)
- ⑪ 2-RIB PL 230x25x1757 (SM570TMC)
- ⑫ 2-RIB PL 230x25x789 (SM570TMC)
- ⑬ 2-RIB PL 230x25x2223 (SM570TMC)
- ⑭ 2-RIB PL 230x25x2252 (SM570TMC)
- ⑮ 2-RIB PL 230x25x2173 (SM570TMC)
- ⑯ 2-RIB PL 230x25x2364 (SM570TMC)
- ⑰ 2-RIB PL 230x25x959 (SM570TMC)
- ⑱ 2-RIB PL 230x25x955 (SM570TMC)
- ⑲ 2-RIB PL 230x25x540 (SM570TMC)
- ⑳ 2-RIB PL 230x25x910 (SM570TMC)
- ㉑ 2-RIB PL 230x25x806 (SM570TMC)
- ㉒ 2-RIB PL 230x25x955 (SM570TMC)
- ㉓ 2-RIB PL 230x25x743 (SM570TMC)
- ㉔ 10-RIB PL 230x25x333 (SM570TMC)

安定器箱固定板 S=1:10

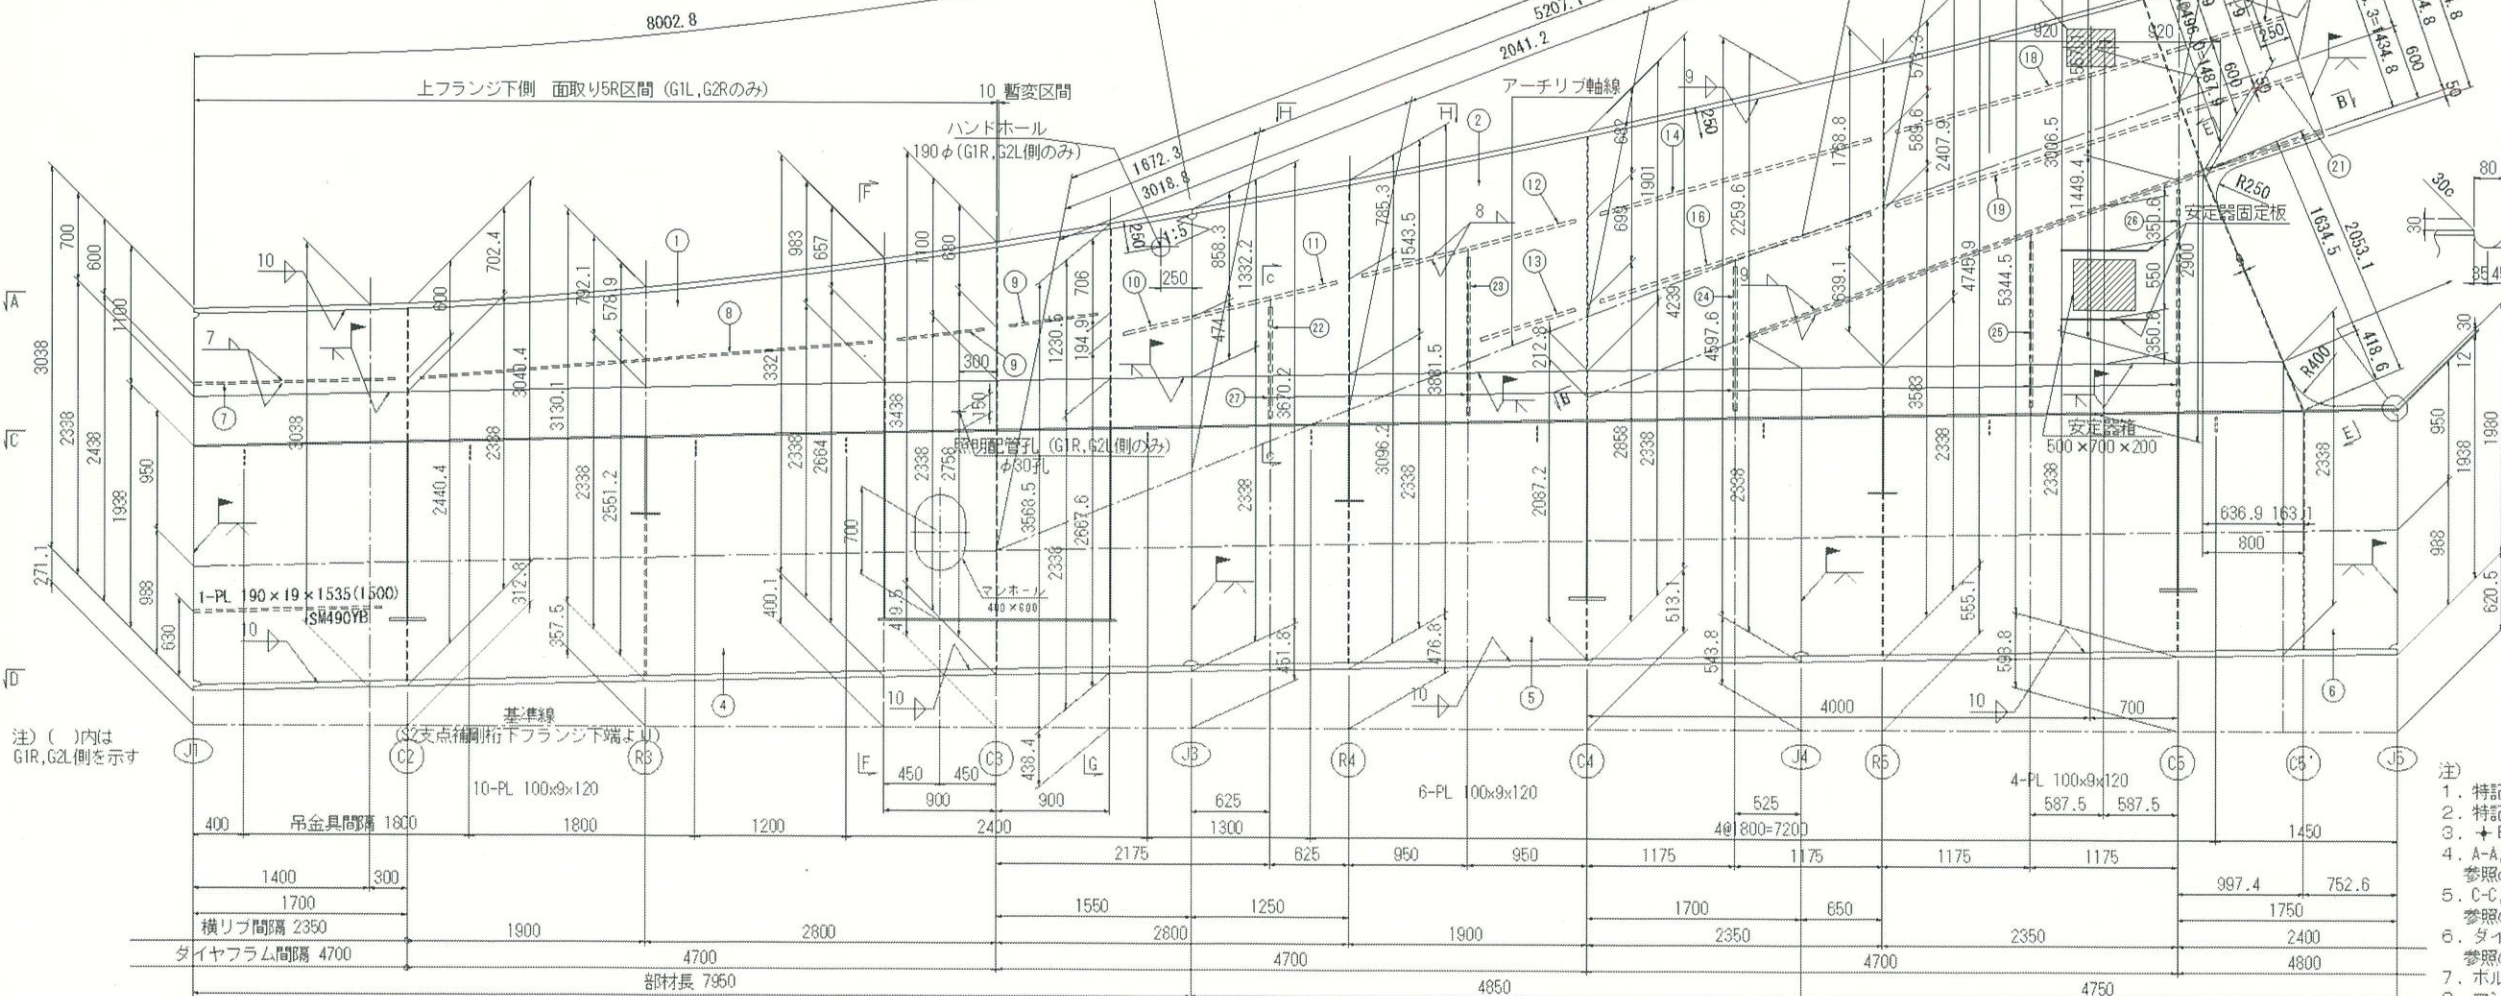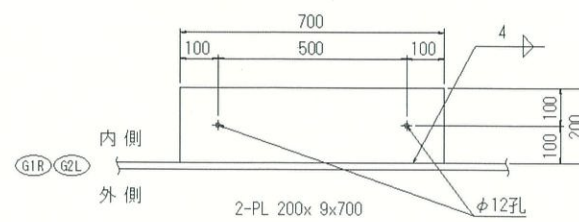

- 1. 特記なき材質は全てSM400Aとする。
- 2. 特記なきスカーラップは全て35Rとする。
- 3. +印はトルシア形高力ボルトM22 (S10T)を示す。
- 4. A-A, B-B, F-F, G-G, H-H, ④部断面はアーチリブ (その1-2) 図を参照のこと。
- 5. C-C, D-D, 縦リブ添付詳細はアーチリブ (その1-3) 図を参照のこと。
- 6. ダイアフラム断面, 横リブ断面はアーチリブ (その1-4) 図を参照のこと。
- 7. ボルト孔を全て26.5φとする。
- 8. マンホール詳細は、アーチリブ (その1-2) "b" を参照のこと。
- 9. 隅角部の梯子詳細は、別紙参照のこと。