



A 1 橋台構造一般図(その1) S=1:100


正面図

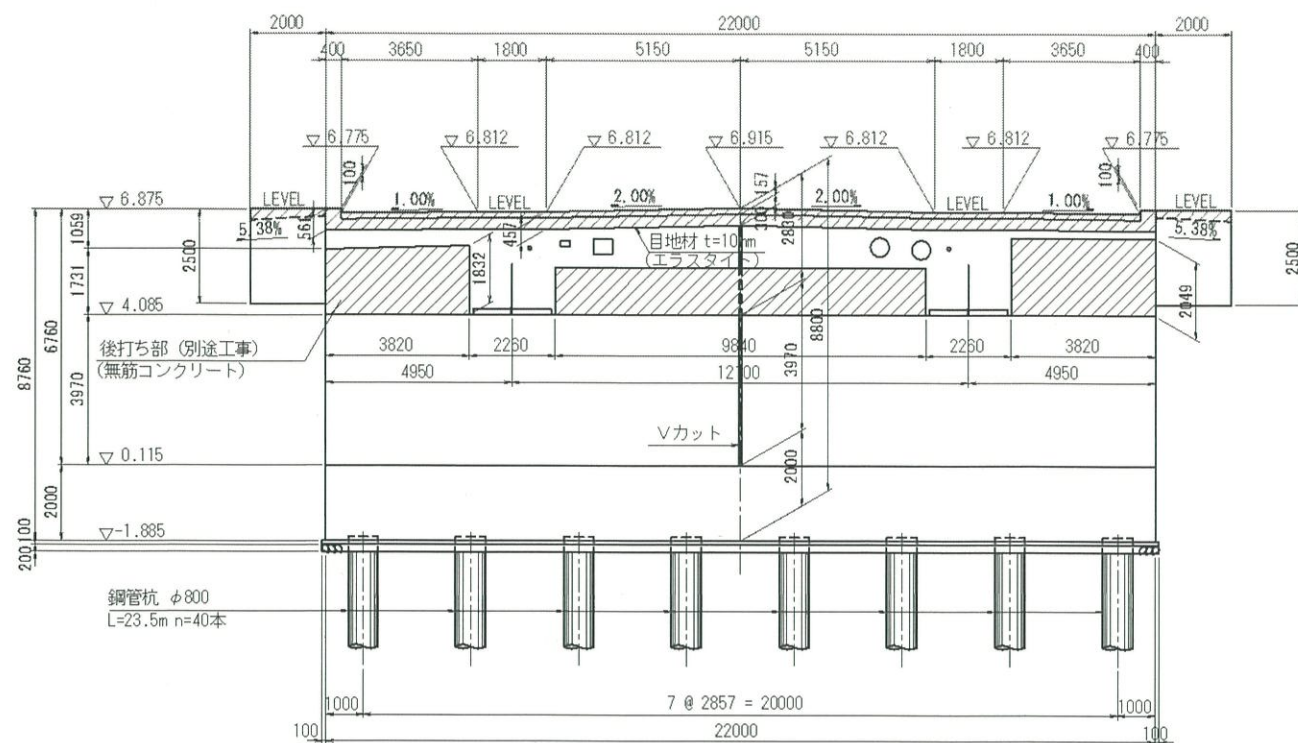


背面図

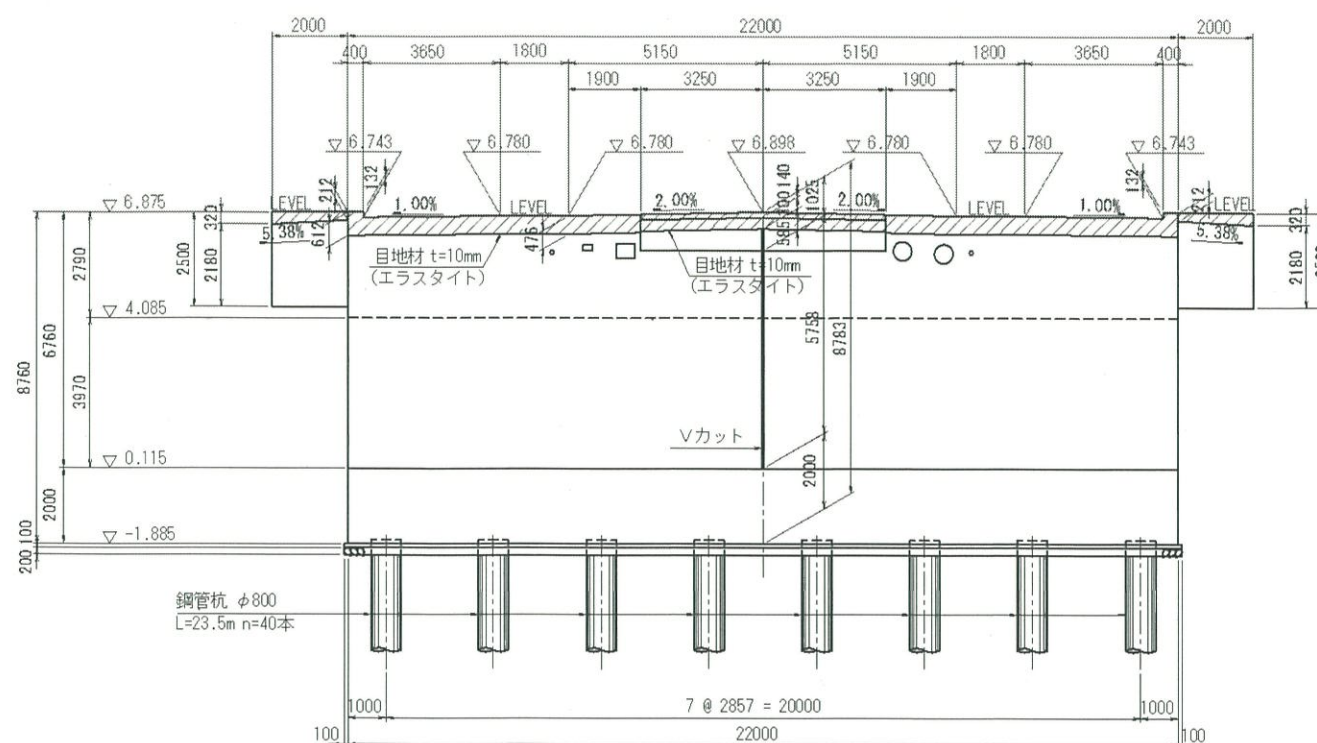


A - A

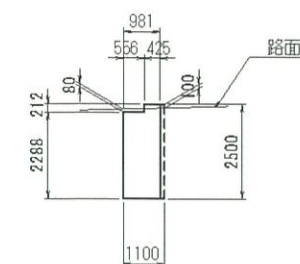


平面図

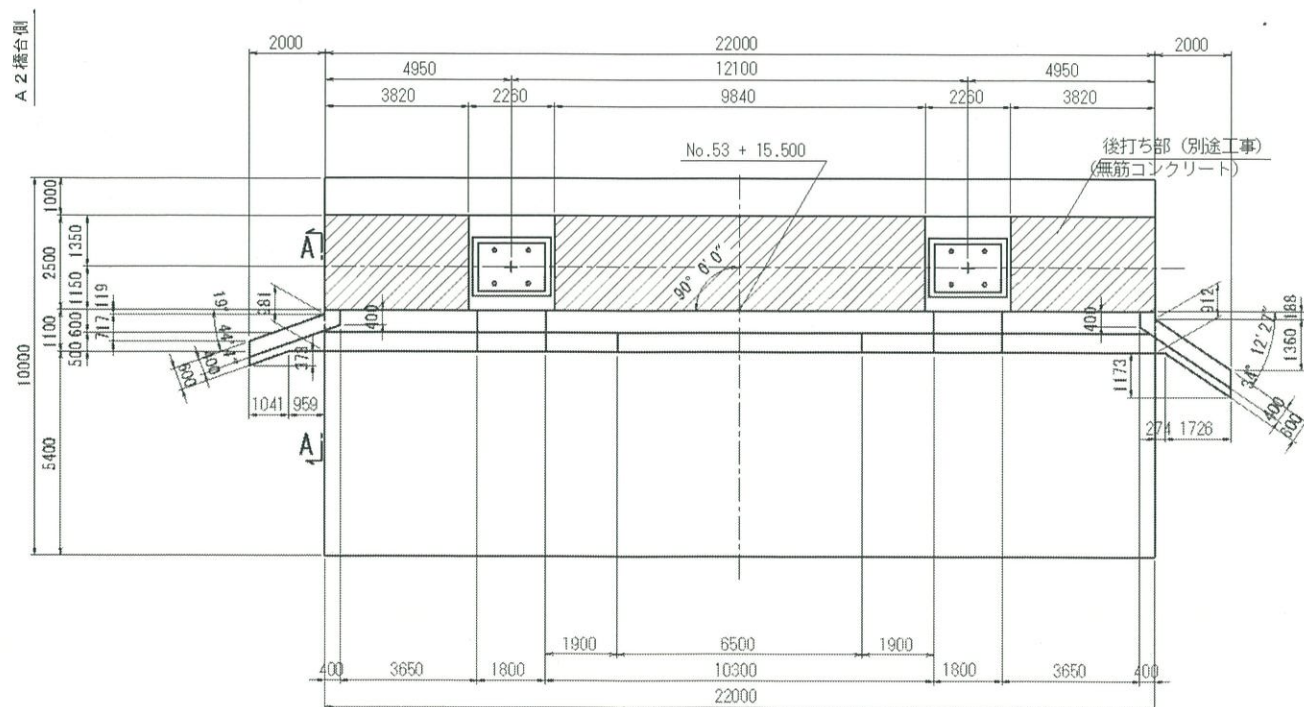

基礎平面図

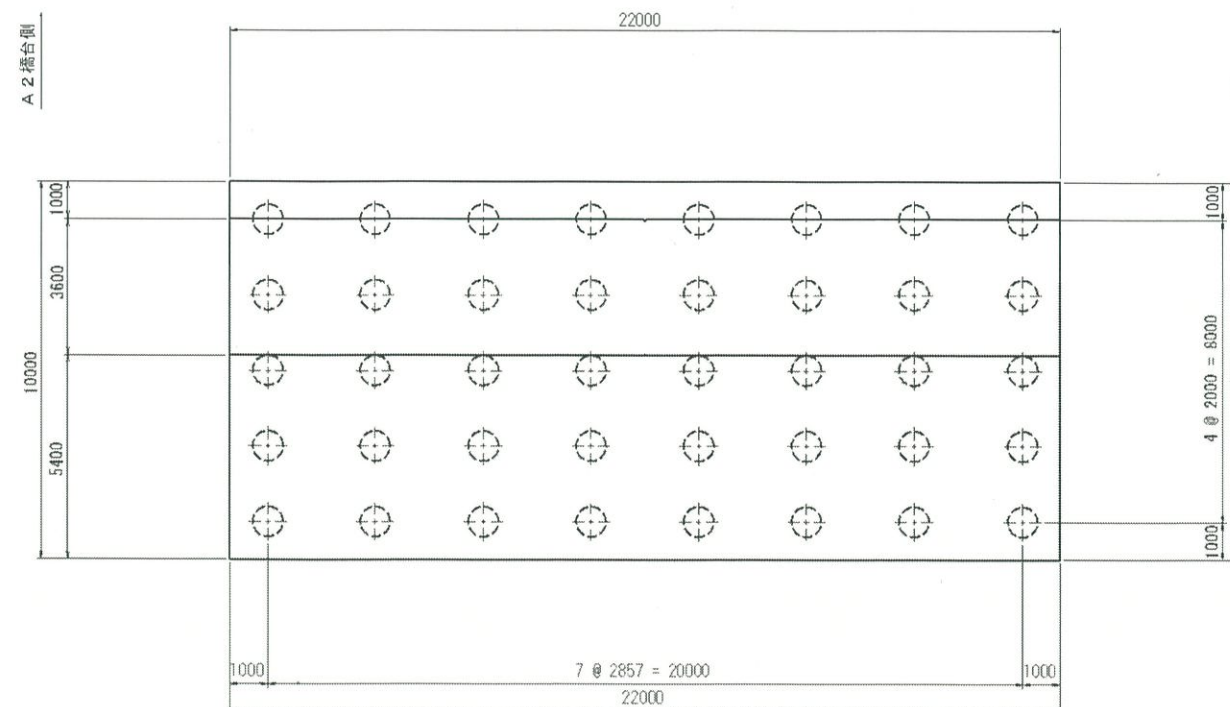

Vカット詳細図 S=1:10

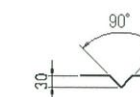

部は、後打ち部 (別途工事) を示す。

日付	UR 都市機構 東京都心支社	部長 次長 部付 チーム リーダー 担当	設計事務所 大日本コンサルタント (株)	工事名称	設計名称 新田豊島橋 (仮称) 実施設計	図面名称 A 1 橋台構造一般図(その1)	縮尺 1:100	図面番号 K-6
----	----------------	----------------------	----------------------	------	----------------------	-----------------------	----------	----------