



アーチリブ (その9-3) S=1:30

C-C

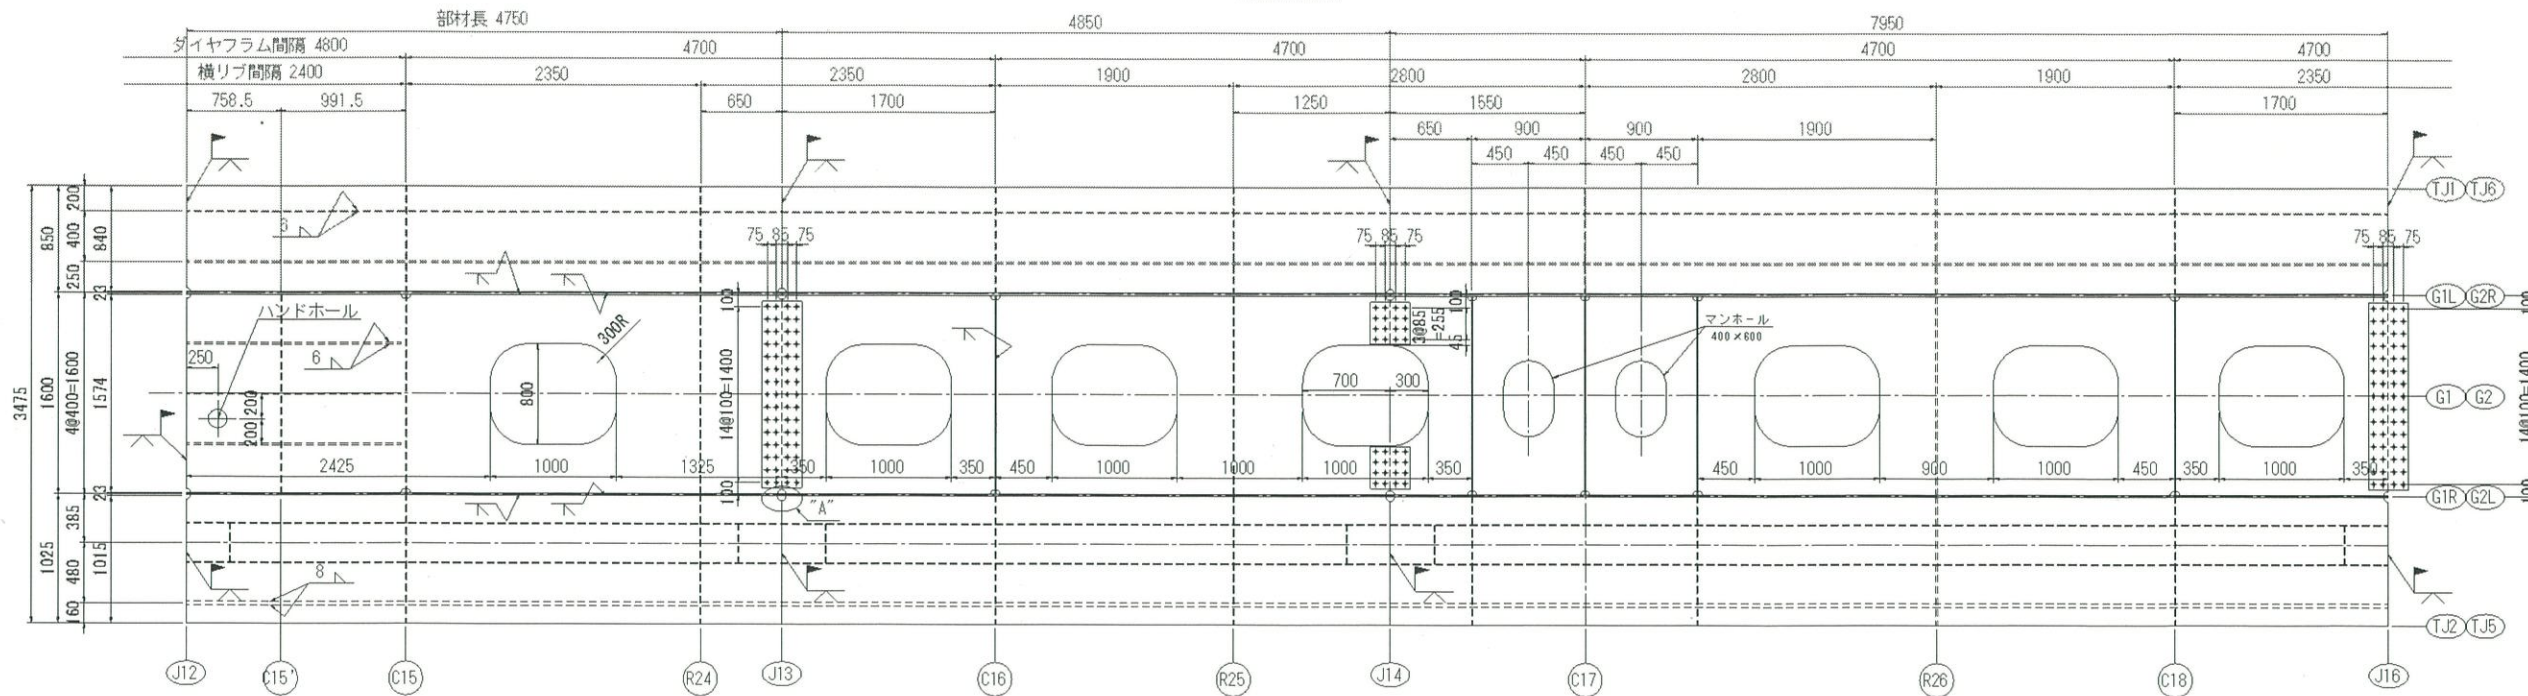


- 1-DECK PL 840x12x4751
- 1-DECK PL 840x12x4851
- 1-DECK PL 840x12x7952
- 1-DECK PL 1015x12x4751 (SM490YA)
- 1-DECK PL 1015x12x4851 (SM490YA)
- 1-DECK PL 1015x12x7952 (SM490YA)
- 1-PL 1574x12x4751
- 1-PL 1574x12x1696
- 1-PL 1574x12x3146
- 1-PL 1574x12x646
- 2-PL 1574x12x891
- 1-PL 1574x12x3792
- 1-PL 1574x12x1696
- 4-SPL PL 315x9x1480 (SS400)
- 4-SPL PL 315x9x335 (SS400)
- 152-TCB M22x65 (S10T)
- 8-PL 60x9x140
- 2-RIB PL 140x14x4741
- 2-RIB PL 140x14x4841
- 2-RIB PL 140x14x7942
- 3-RIB PL 140x14x1706
- 1-RIB PL 200x25x4741 (SM490YB)
- 1-RIB PL 200x25x4841 (SM490YB)
- 1-RIB PL 200x25x7942 (SM490YB)
- 1-U RIB 320x260x6x4741 (SM490YA)
- 1-U RIB 320x260x6x4841 (SM490YA)
- 1-U RIB 320x260x6x7942 (SM490YA)
- 6-PL 254x8x308 (SM490YA)

D-D

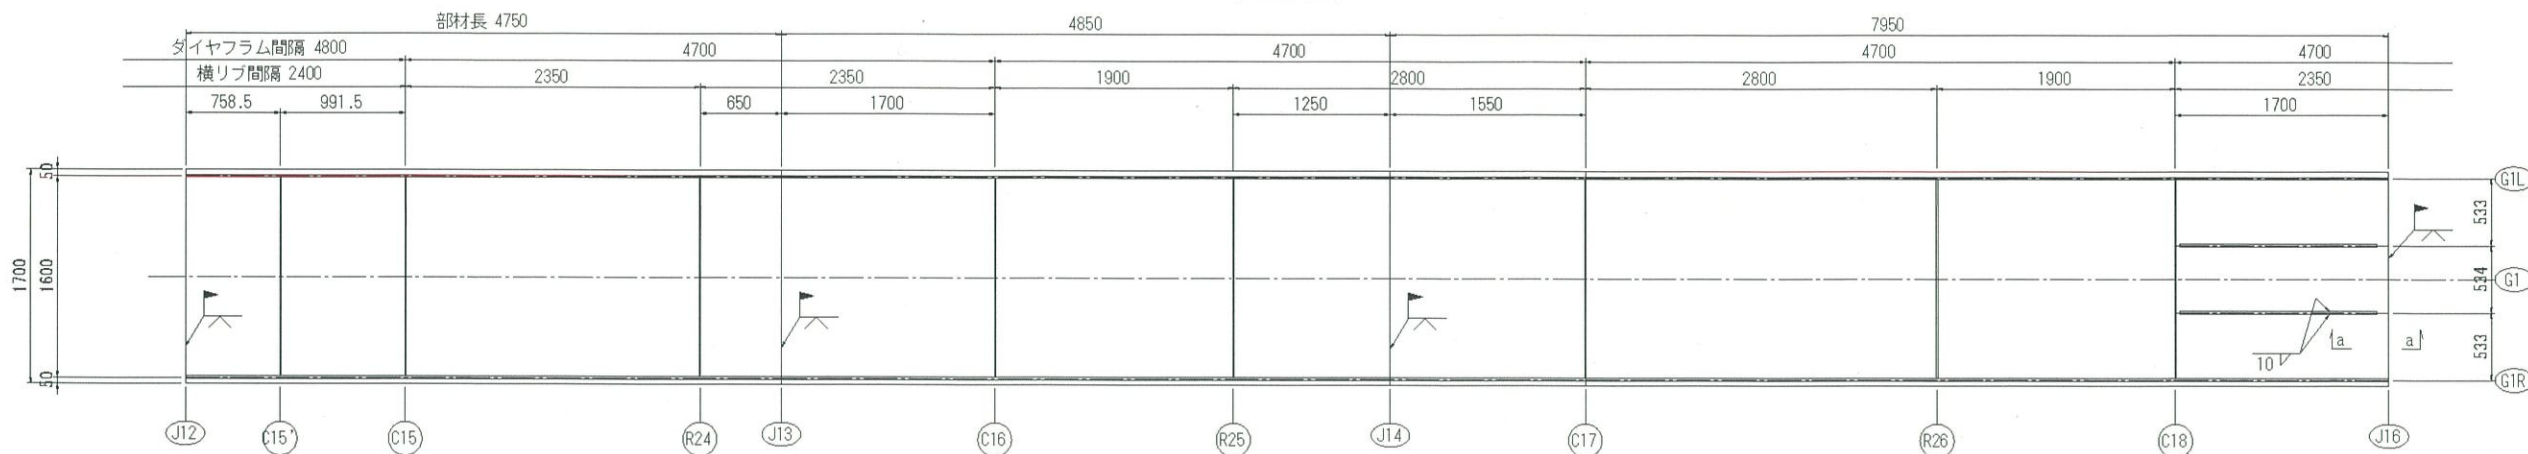


- 1-FLG PL 1700x48x4751 (SM570TMC-H)
- 1-FLG PL 1700x48x4851 (SM570TMC-H)
- 1-FLG PL 1700x48x7952 (SM570TMC-H)
- 2-RIB PL 230x25x1566 (SM570TMC)

"A"部詳細 S=1:10

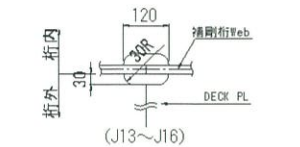


縦リブ添接詳細


アーチリブ部

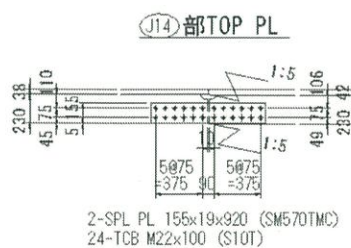


DECK部

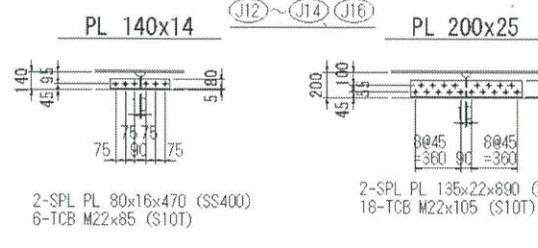


WEB水平継手部

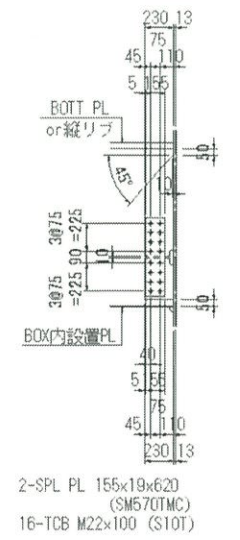


a-a S=1:10

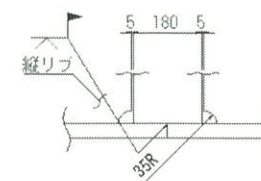

スカーラップ詳細図

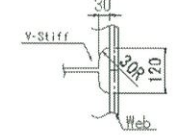

配置図 S=1:300

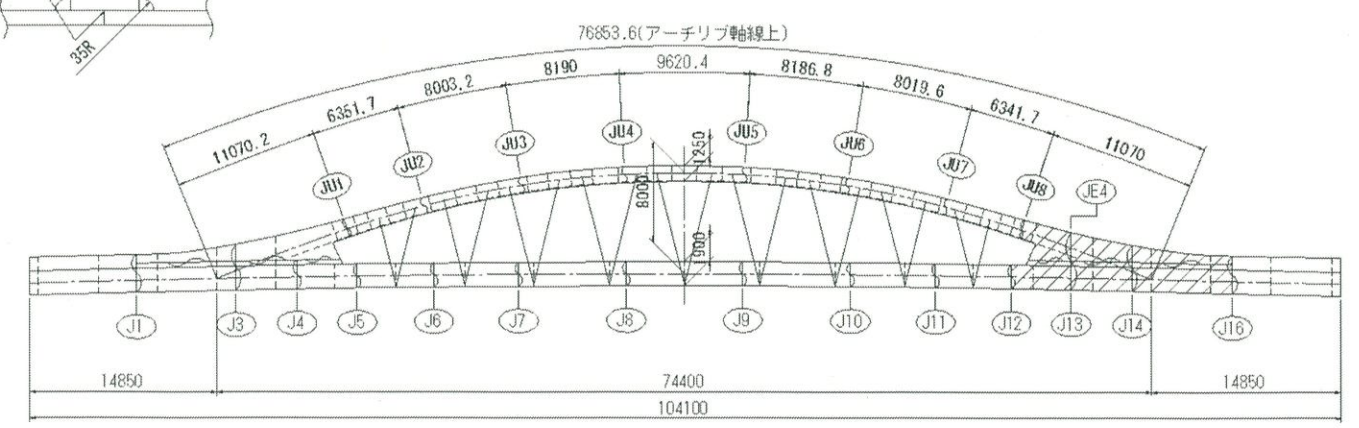

- 注
- 1. 特記なき材質は全てSM400Aとする。
- 2. 特記なきスカーラップは全て3Rとする。
- 3. +印はトルシア形高力ボルトM22 (S10T) を示す。
- 4. マンホール詳細は アーチリブ (その9-2) "a" を参照のこと。

日付



都市機構 東京都心支社

部長

次長

チームリーダー

担当

設計事務所

大日本コンサルタント(株)

工事名称

新田三丁目地区開発新田豊島橋(仮称)
上部工建設工事(第1回変更)

設計名称

新田豊島橋(仮称)実施設計

図面名称

アーチリブ (その9-3)

縮尺

図示

図面番号

J-52