
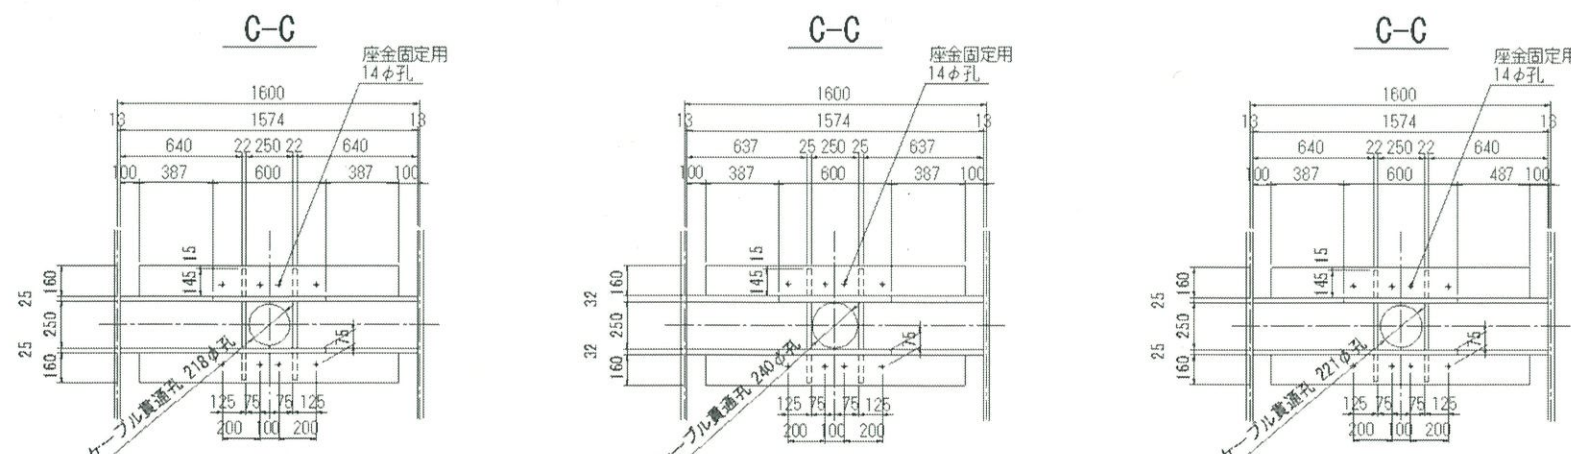
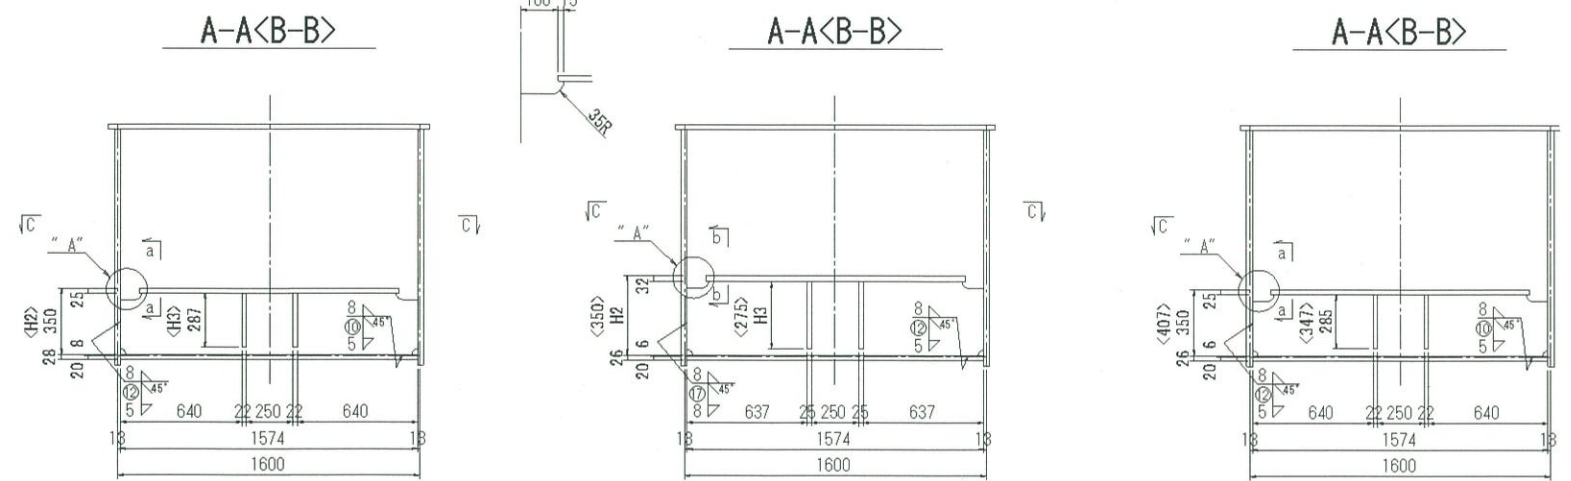



アーチリブ (その10-3) S=1:20

吊り材定着部詳細 (その3)

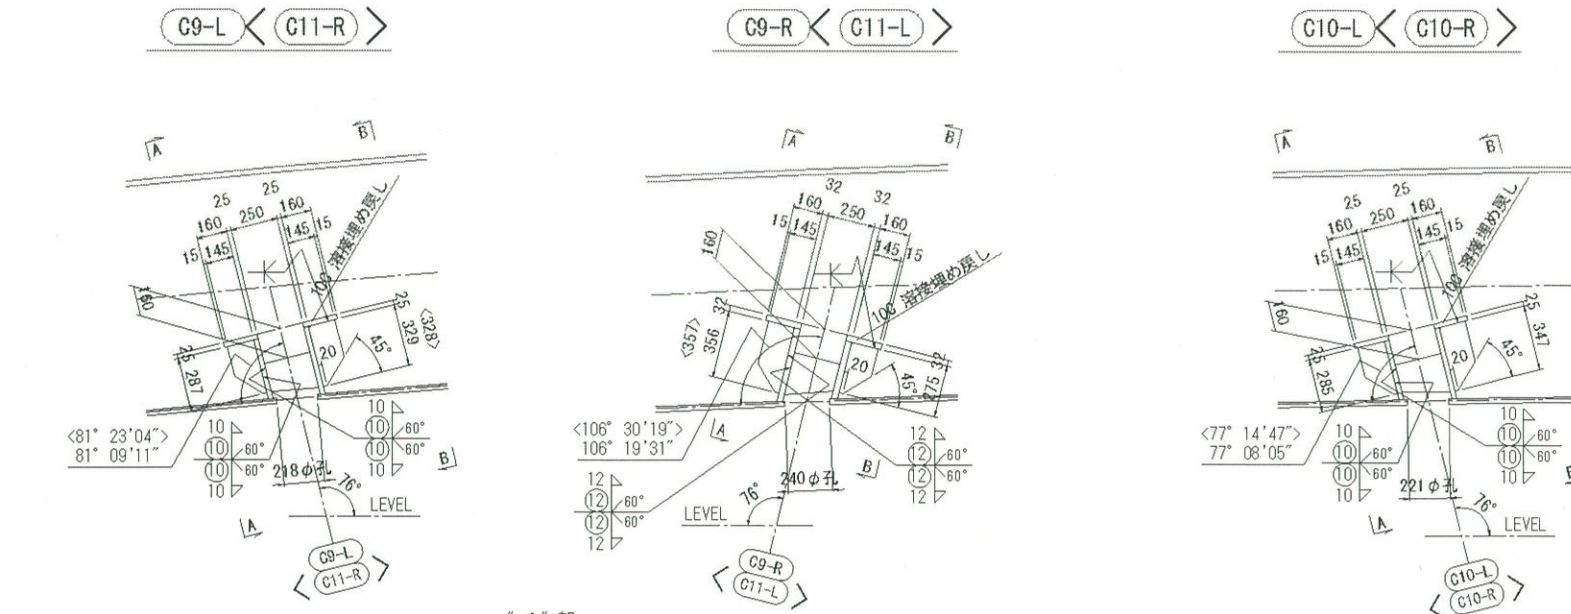


1-WEB PL 325x25x1574 (SM490YB)	1-WEB PL 325x25x1574 (SM490YB)	1-WEB PL 325x25x1574 (SM490YB)	1-WEB PL 325x25x1574 (SM490YB)
1-WEB PL H1x25x1574 (SM490YB)	1-WEB PL H1x25x1574 (SM490YB)	1-WEB PL H1x25x1574 (SM490YB)	1-WEB PL H1x25x1574 (SM490YB)
2-FLG PL 185x25x1574 (SM490YB)	2-FLG PL 185x25x1574 (SM490YB)	2-FLG PL 185x25x1574 (SM490YB)	2-FLG PL 185x25x1574 (SM490YB)
2-RIB PL 145x22x287 (SM490YB)	2-RIB PL 145x22x287 (SM490YB)	2-RIB PL 145x22x287 (SM490YB)	2-RIB PL 145x22x287 (SM490YB)
2-RIB PL 145x22xH3 (SM490YB)	2-RIB PL 145x22xH3 (SM490YB)	2-RIB PL 145x22xH3 (SM490YB)	2-RIB PL 145x22xH3 (SM490YB)
2-RIB PL 250x22x t (SM490YB)	2-RIB PL 250x22x t (SM490YB)	2-RIB PL 250x22x t (SM490YB)	2-RIB PL 250x22x t (SM490YB)

定着座金詳細 S=1:10


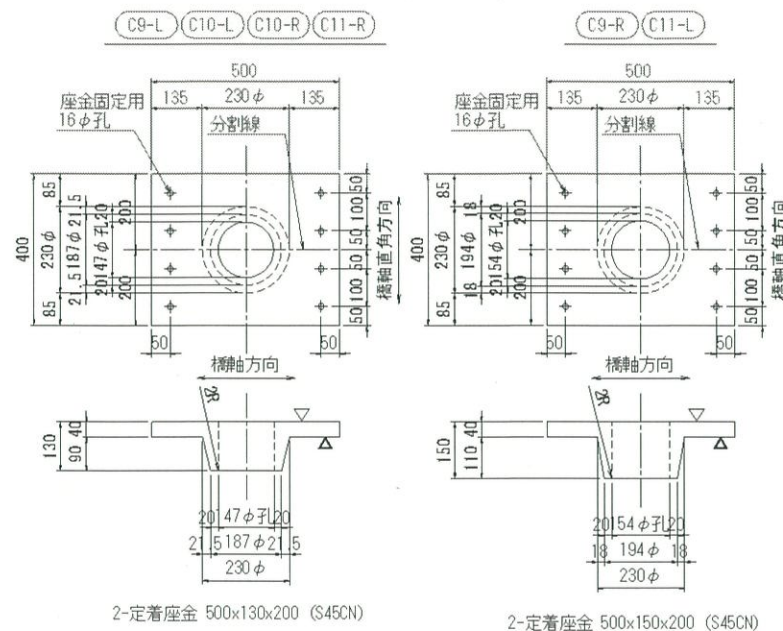


吊材貫通孔部補強板詳細 S=1:10

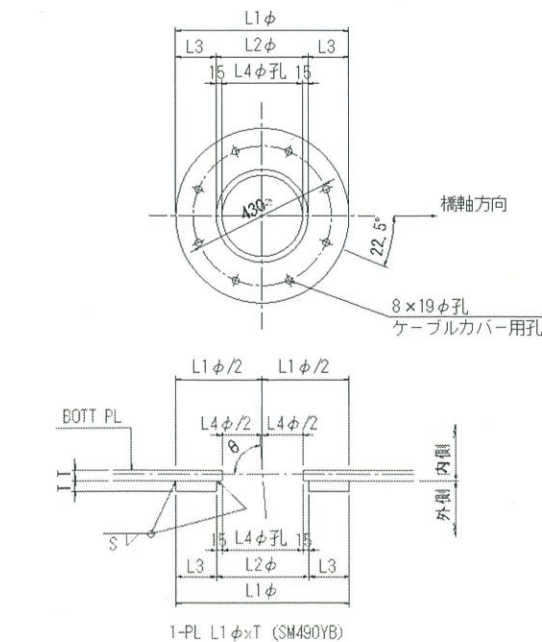

	L1	L2	L3	L4	T	S	θ
C9-L	522	248	137	218	28	8	81° 09'11"
C9-R	554	270	142	240	26	-	106° 19'31"
C10-L	522	251	135.5	221	-	-	77° 08'05"
C10-R	-	-	-	-	-	-	77° 14'47"
C11-L	554	270	142	240	-	-	106° 30'19"
C11-R	522	248	137	218	28	-	81° 23'04"

配置図 S=1:300

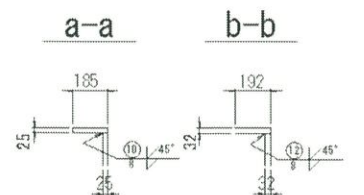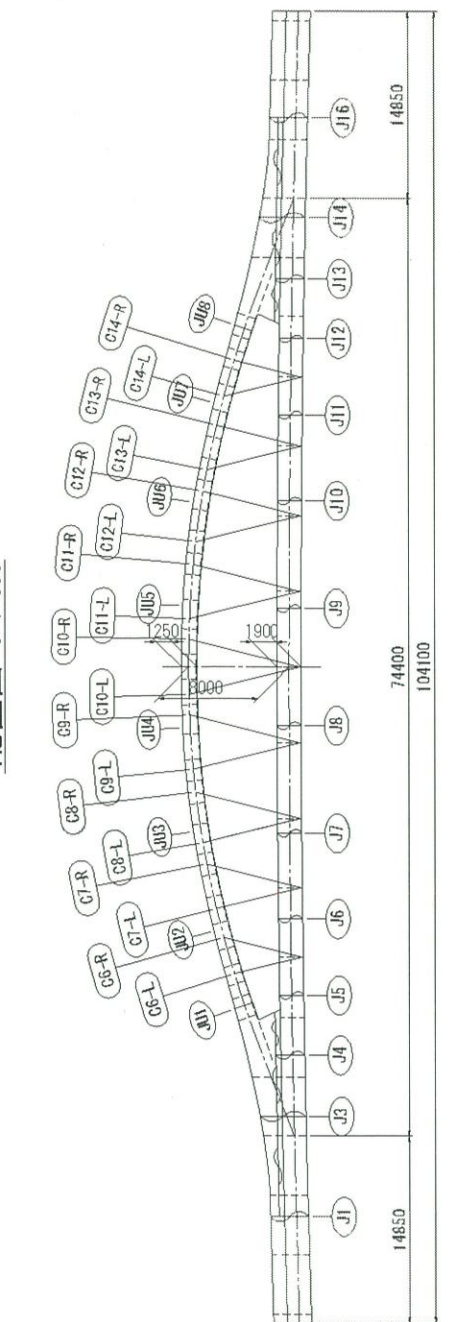

- 注)
- 特記なき材質は全てSM400Aとする。
 - 特記なきスカーラップは全て36Rとする。
 - 印はトルシア形高力ボルトM22 (S10T) を示す。
 - 各種詳細図は共通詳細図を参照のこと。
 - *印は耐震垂鉛メッキを施す。