

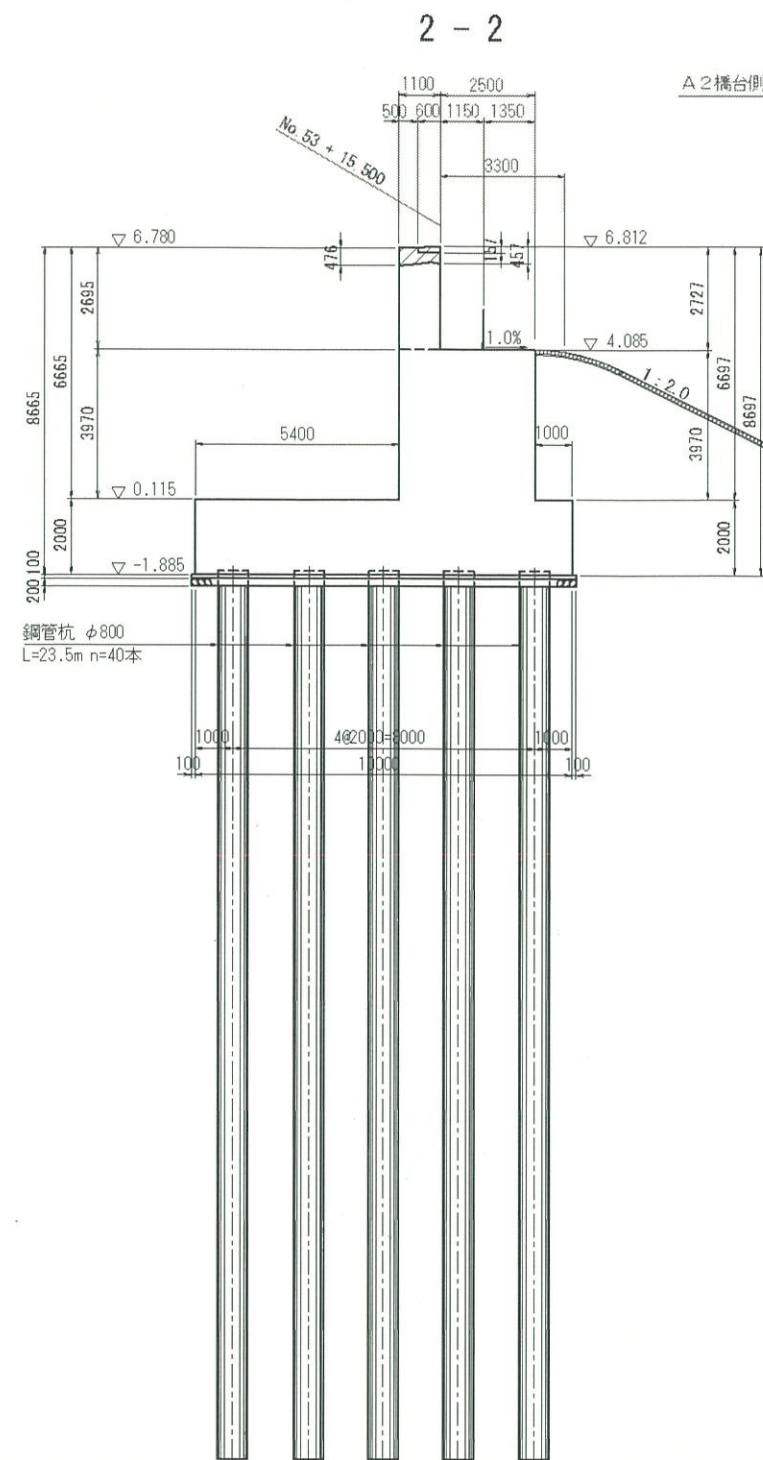


A 1 橋台構造一般図(その2) S=1:100

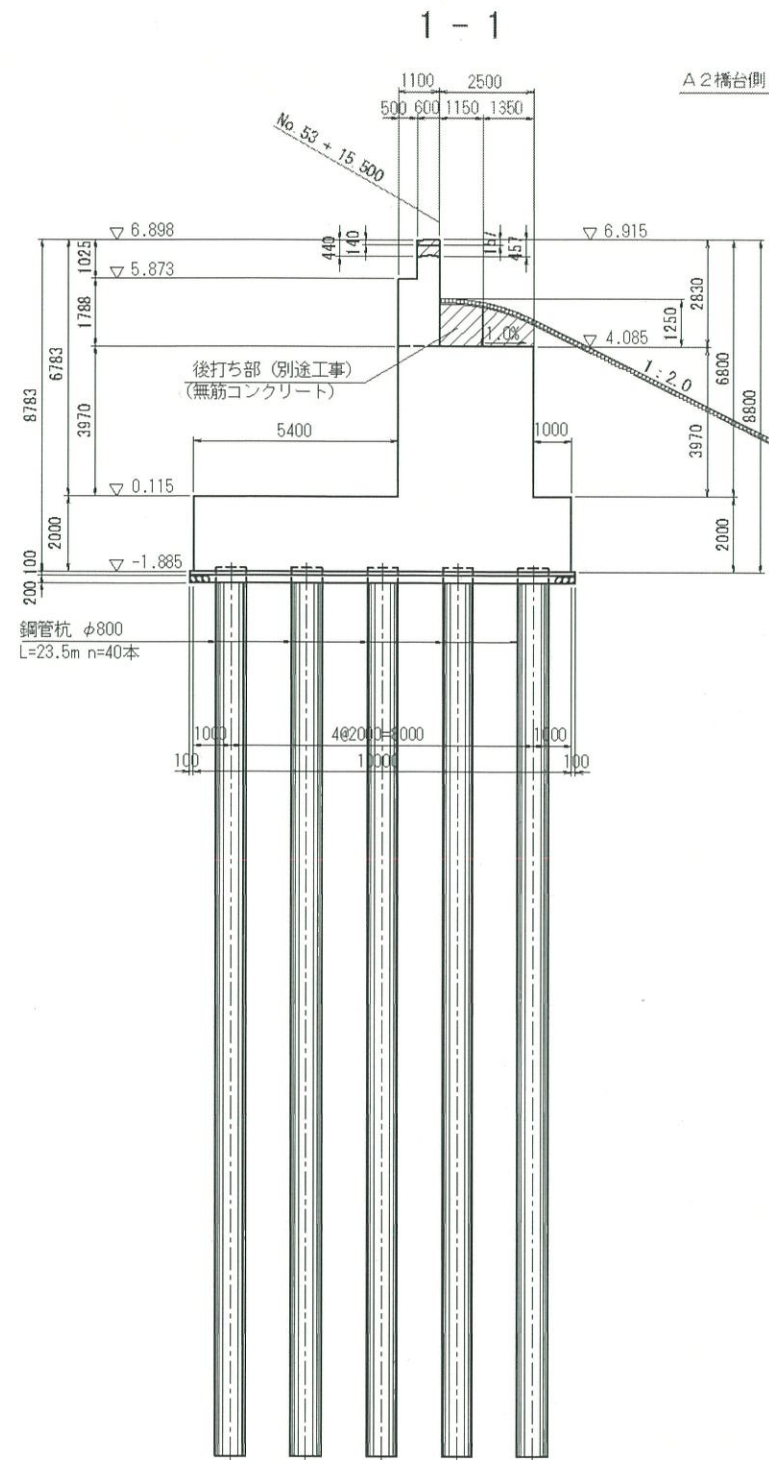

位置図

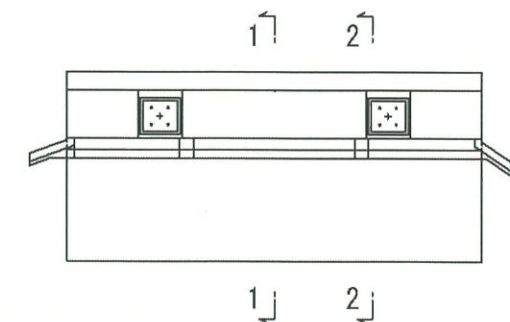

//// 部は、後打ち部 (別途工事) を示す。

日付	都市機構 東京都心支社	部長 次長 部付 チームリーダー 担当	設計事務所 大日本コンサルタント (株)	工事名称 新田豊島橋 (仮称) 実施設計	設計名称 A 1 橋台構造一般図(その2)	図面番号 K-7	縮尺 1:100
----	-------------	---------------------	-------------------------	-------------------------	--------------------------	-------------	-------------