



A 2 橋台構造一般図(その3) S=1:50


正面図

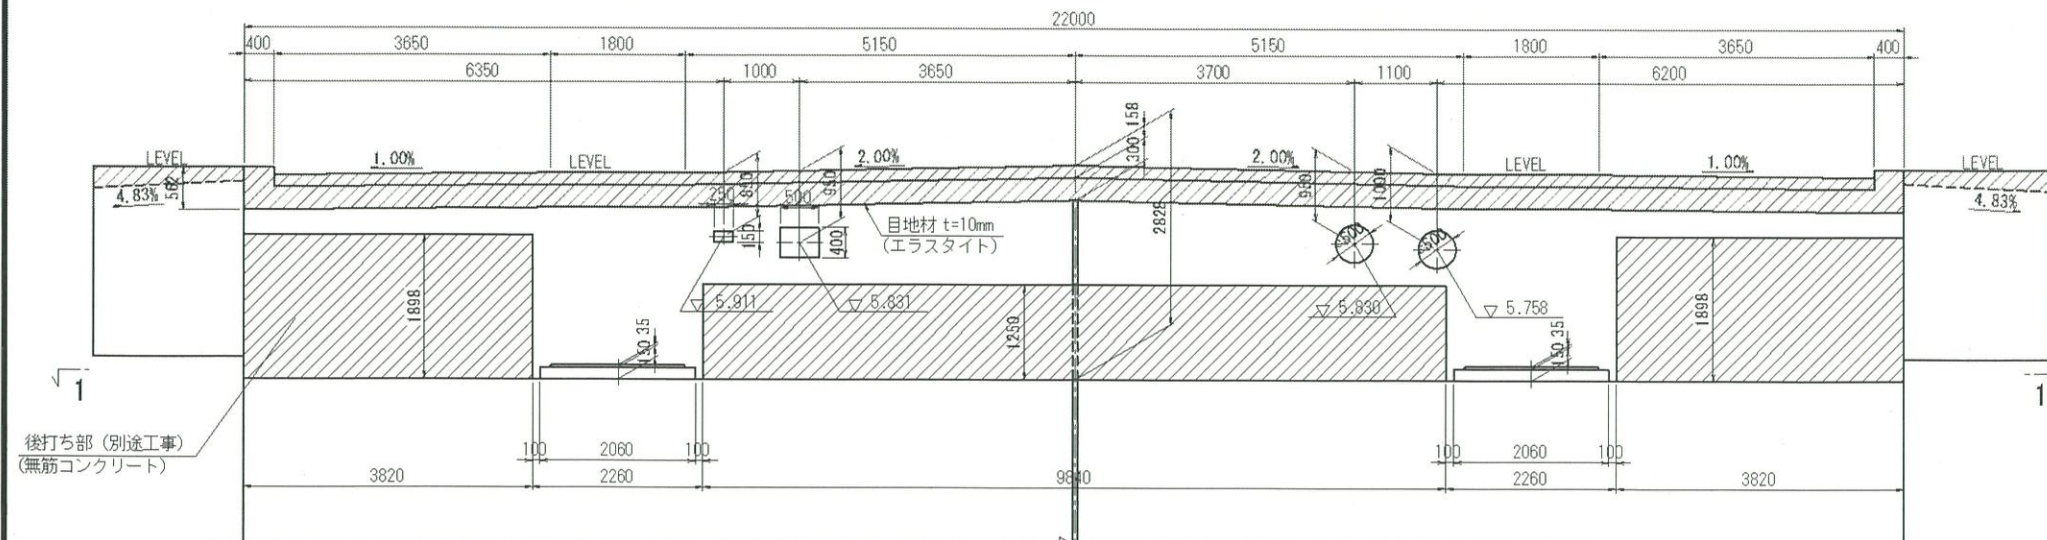


背面図

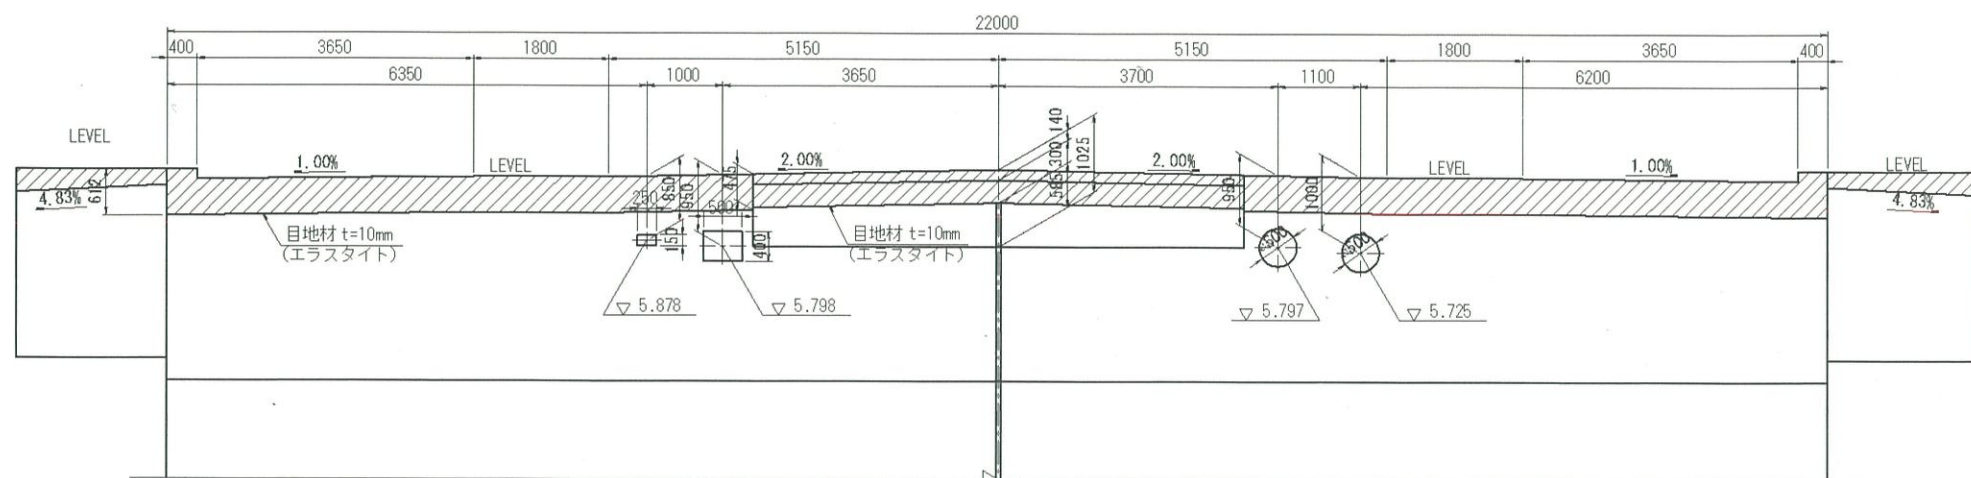

1 - 1

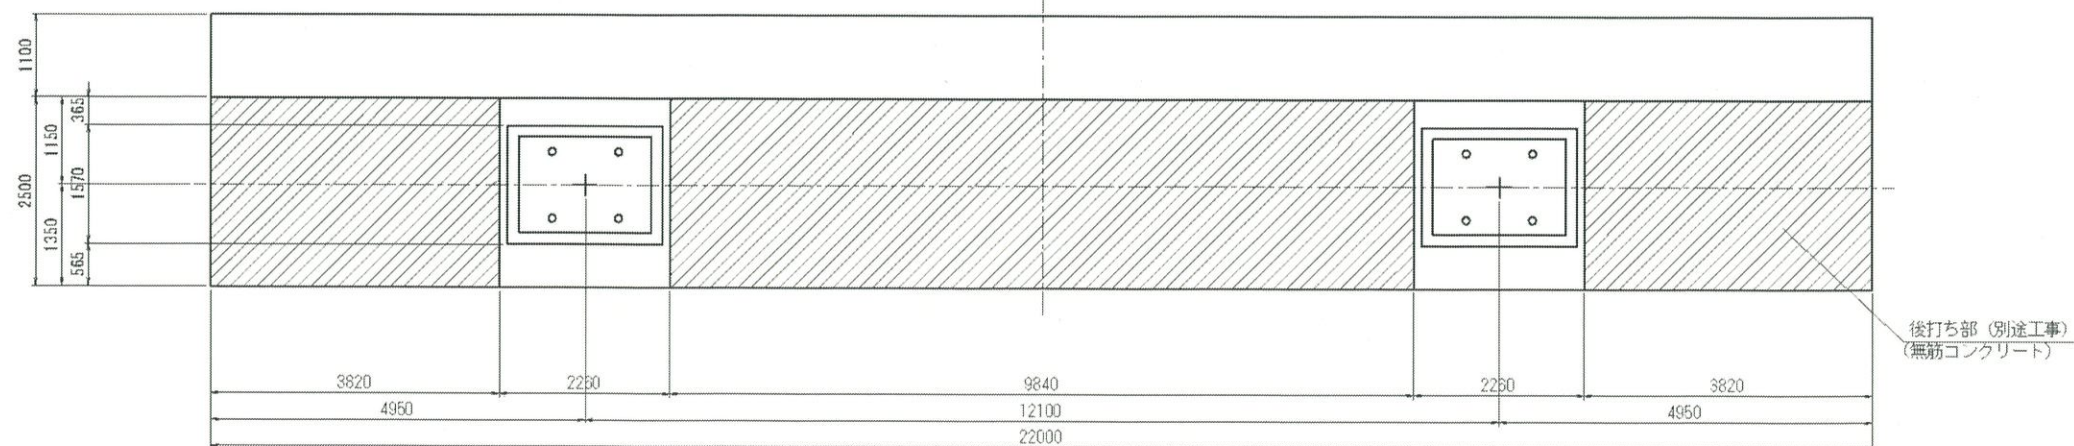


断面図

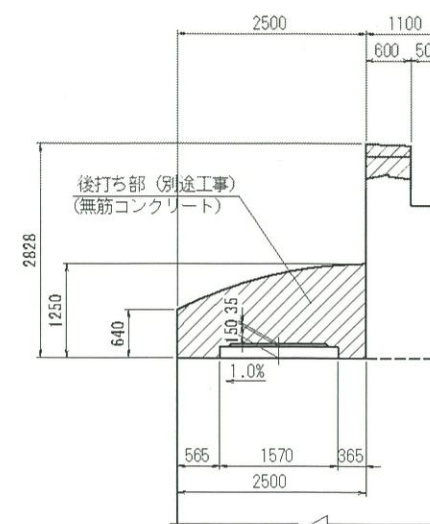


ノックオフ部詳細図 S=1:30


車道部

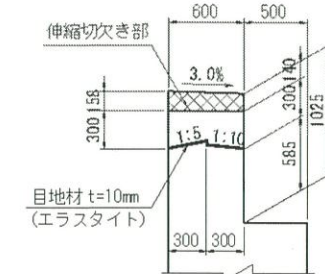


歩道部

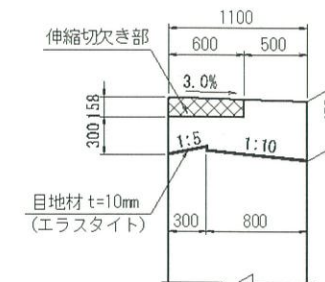

支承箱抜き詳細図 S=1:30

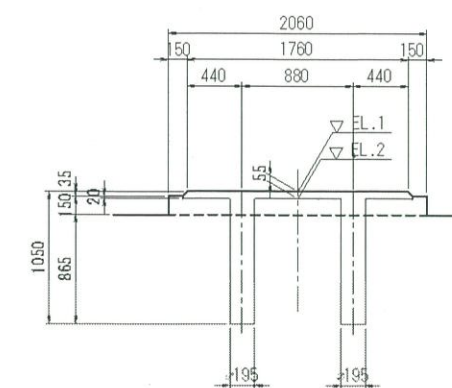

	G1	G2
EL.1	4.211	4.211
EL.2	4.156	4.156
モルタル厚	35	35
台座高	150	150
下部工天端高	4.026	4.026

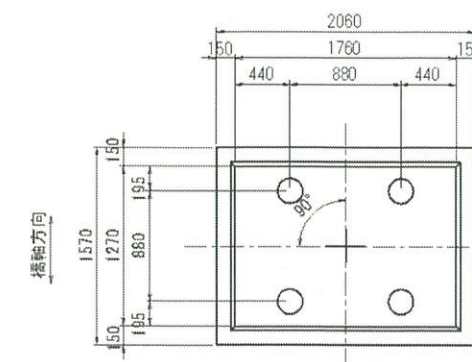

 部は、後打ち部（別途工事）を示す。