



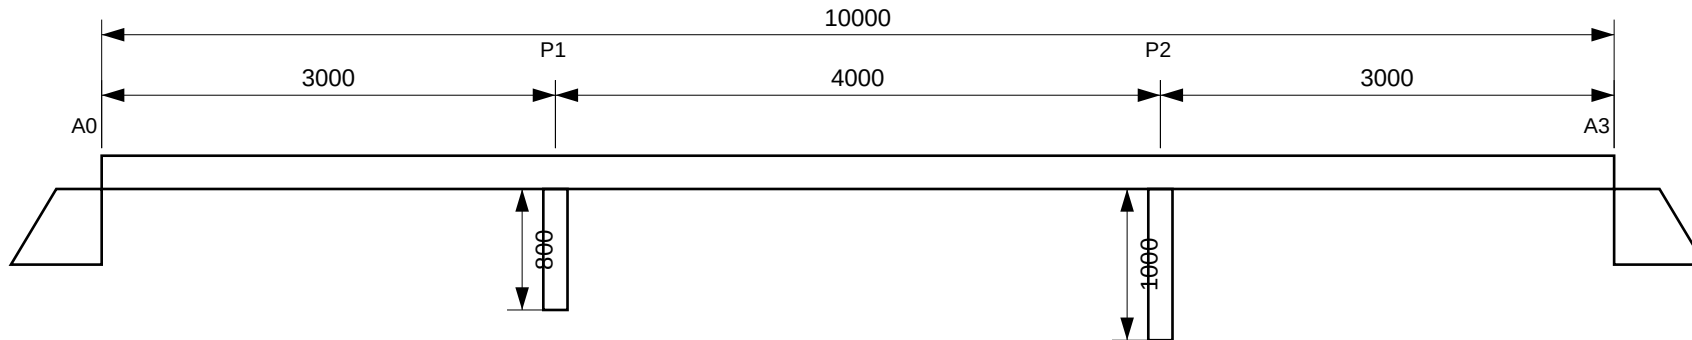

NOTES 说明:

- 尺寸单位: cm, 高程单位: m (DIMENSIONS IN cm)
- 跨径布置 SPANS: 30+40+30 m
- 墩高 PIER HEIGHTS: P1=8 m, P2=10 m
- 支座 BEARINGS: A0 双向活动, P1 固定, P2 纵向活动, A3 双向活动
- 主梁 DECK: C50; 桥墩 PIER: C40; 容重 UNIT WEIGHT 26 kN/m³
- 二期恒载 SECONDARY DEAD LOAD: 45 kN/m
- 车道荷载 LANE LOAD: $q_k=10.5$ kN/m, $P_k=320$ kN, 2 LANES
- 单元长度 ELEMENT SIZE: 2 m


PROJECT	XX RIVER BRIDGE 某河大桥
TITLE	总体布置图 GENERAL ARRANGEMENT
SCALE	1:500
UNITS	cm
SHEET	1/3

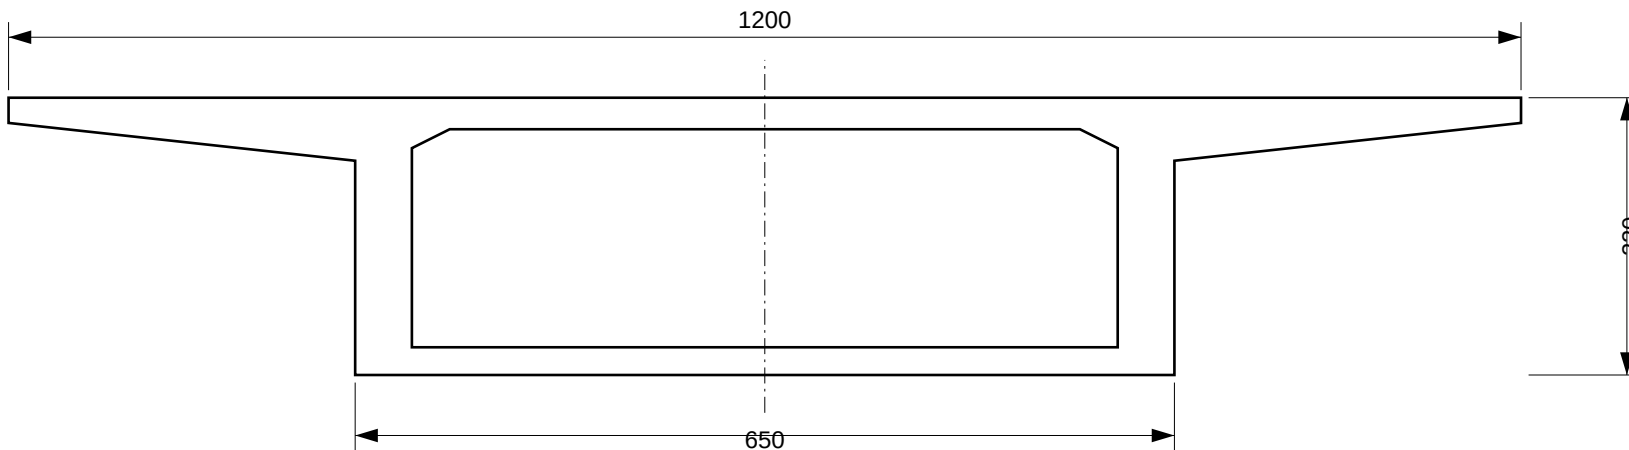

NOTES 说明:

- 尺寸单位: cm
- 单箱单室 SINGLE-CELL BOX, C50

PROJECT	XX RIVER BRIDGE 某河大桥
TITLE	主梁横断面 GIRDER CROSS SECTION
SCALE	1:60
UNITS	cm
SHEET	2/3

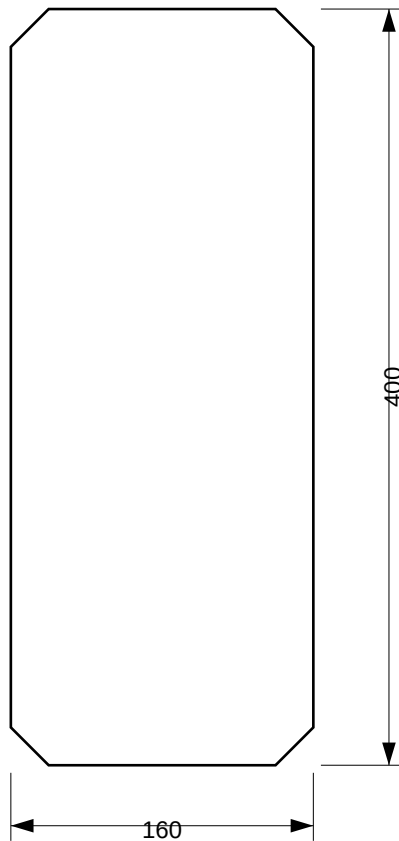

NOTES 说明:

- 尺寸单位: cm
- 倒角 CHAMFER 20x20, C40
- 横向 TRANSVERSE = vertical on this sheet

PROJECT	XX RIVER BRIDGE 某河大桥
TITLE	桥墩断面 PIER SECTION
SCALE	1:40
UNITS	cm
SHEET	3/3