



防護柵 (その2)


高欄取付詳細図 S=1/6

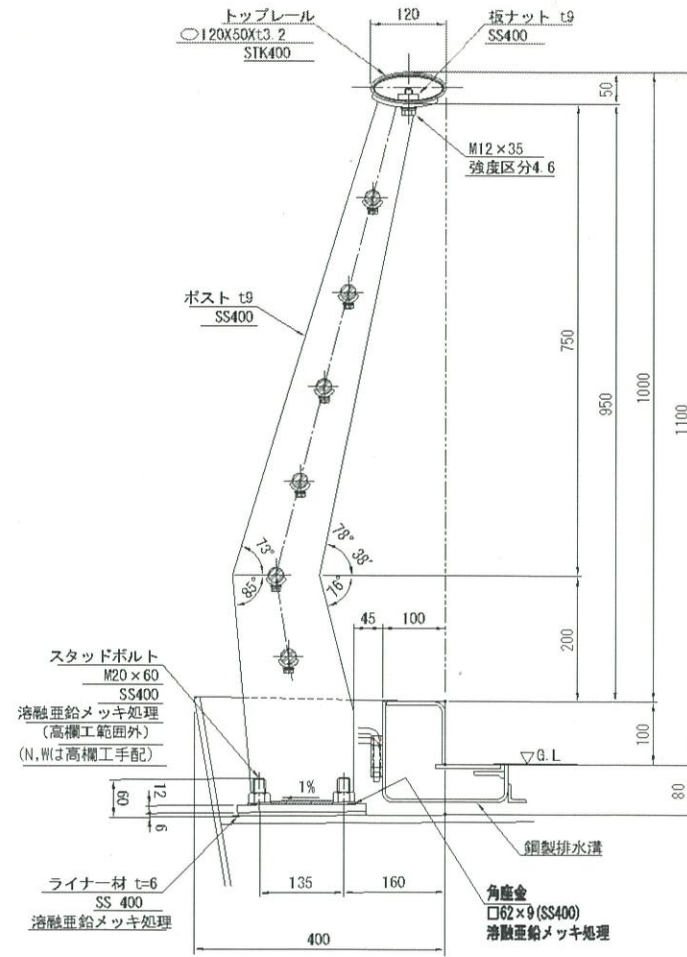


継手部

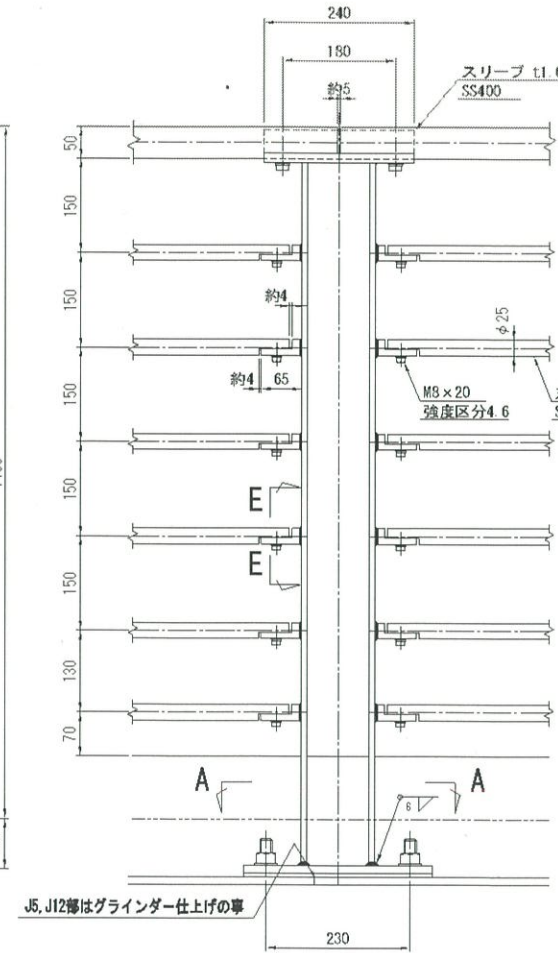


端部

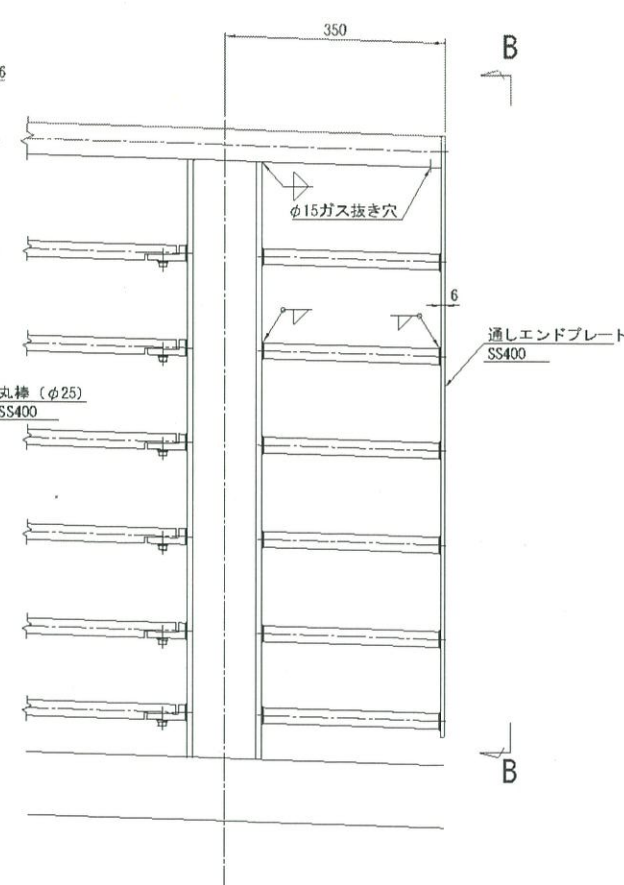


矢視B-B

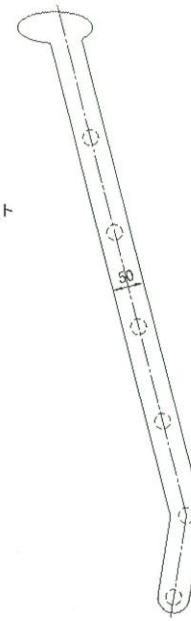


断面E-E S=1/2

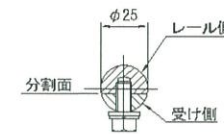

勾配部定着詳細図

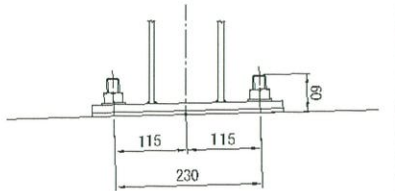

断面A-A

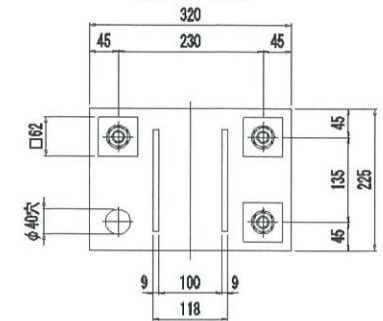

- 注記
1. 本高欄の表面処理は溶融亜鉛メッキ (HDZ35) 処理後、粉体塗装仕上げとする。
 2. 本高欄の設計仕様は「防護柵の設置基準・同解説」(平成16年3月(社)日本道路協会)による。
 3. 塗装色はブラウン(目録S23-255・マンセル近似値5YR2/1.5)とする。

日付



都市機構 東京都心支社

部長

次長

チームリーダー

担当

設計事務所

大日本コンサルタント(株)

工事名称

新田三丁目地区開通新田豊島橋(仮称)
上部工建設工事(第1回変更)

設計名称

新田豊島橋(仮称)実施設計

図面名称

防護柵(その2)

縮尺

図示

図面番号

J-94