




C3鉄筋の本数（材料は主桁にて計上）

	本 数			
	G1	G2	G1	G2
GE1 ~ JE1	30	6	30	6
JE1 ~ J1	28	6	28	6
J1 ~ J3	60	0	60	0
J3 ~ J4	28	12	28	12
J4 ~ J5	32	6	32	6
J5 ~ J6	44	4	44	4
J6 ~ J7	54	0	54	0
J7 ~ J8	62	6	62	6
J8 ~ J9	64	12	68	12
J9 ~ J10	62	6	62	6
J10 ~ J11	54	0	54	0
J11 ~ J12	44	4	44	4
J12 ~ J13	32	6	32	6
J13 ~ J14	28	12	28	12
J14 ~ J16	60	0	60	0
J16 ~ JE2	28	6	28	6
JE2 ~ GE2	30	6	30	6
合 計	740	92	744	92
	1668			


注記）※印は照明柱設置部を示す。

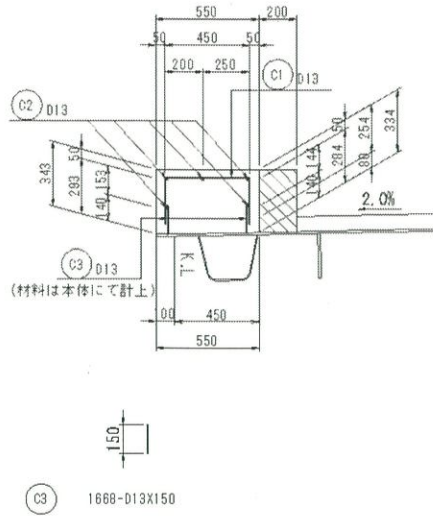


地 覆 配 筋 図 (参考図) S=1:20

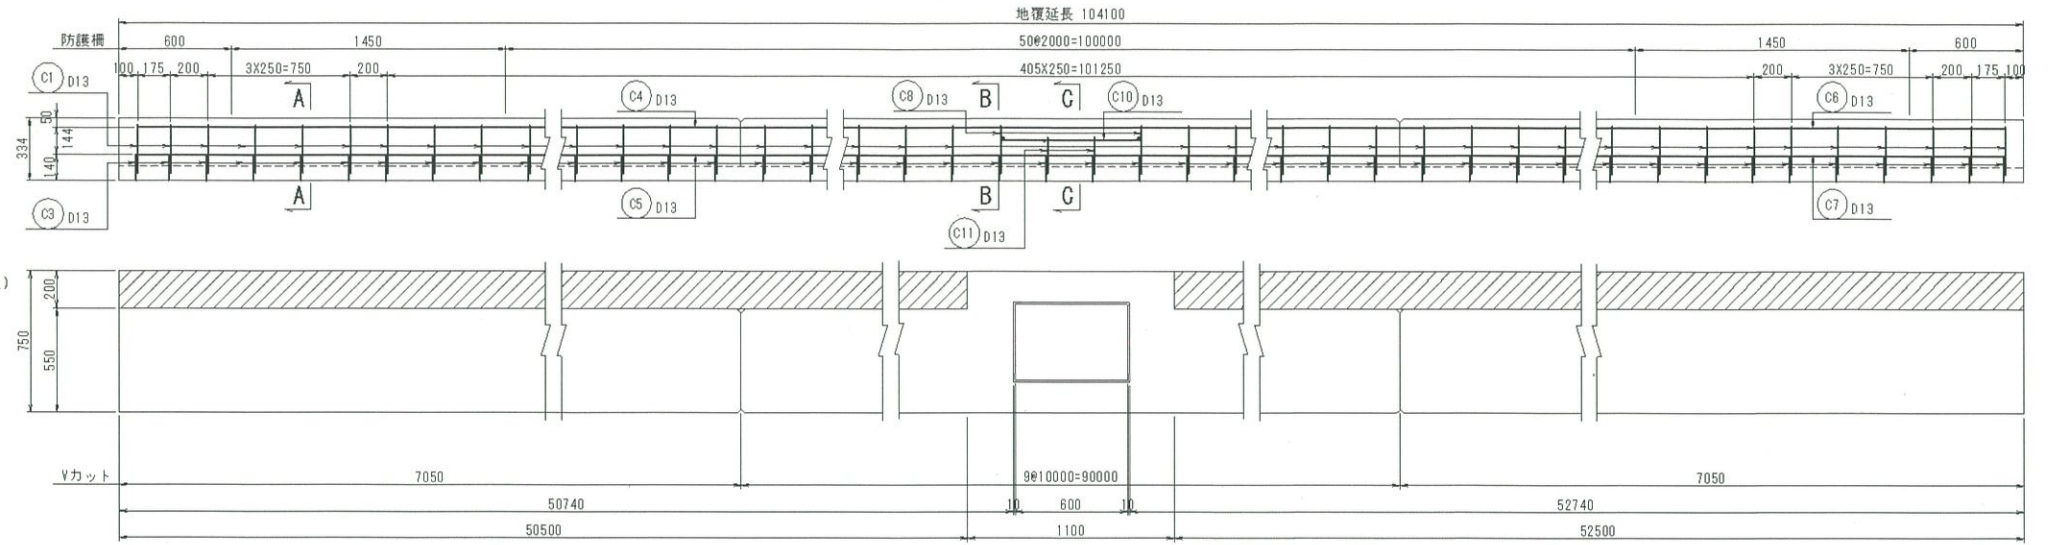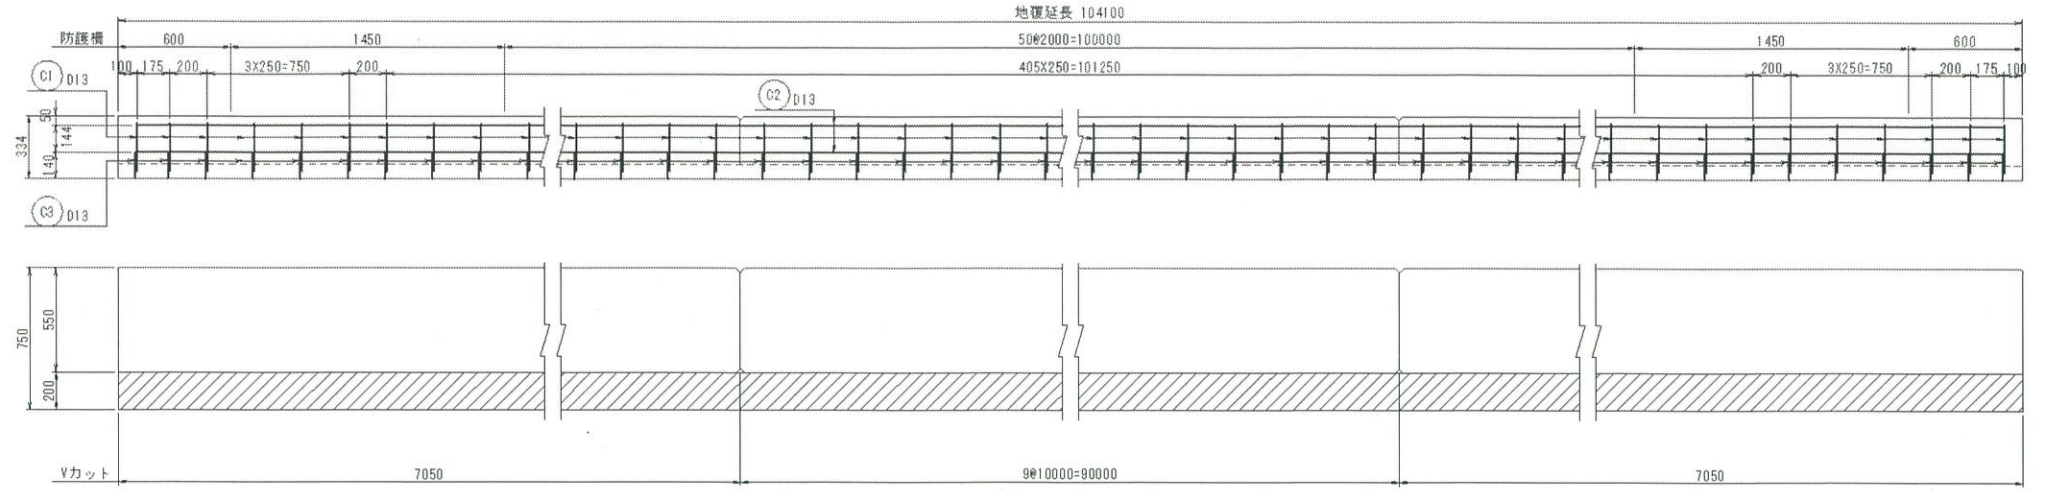

加工鉄筋図

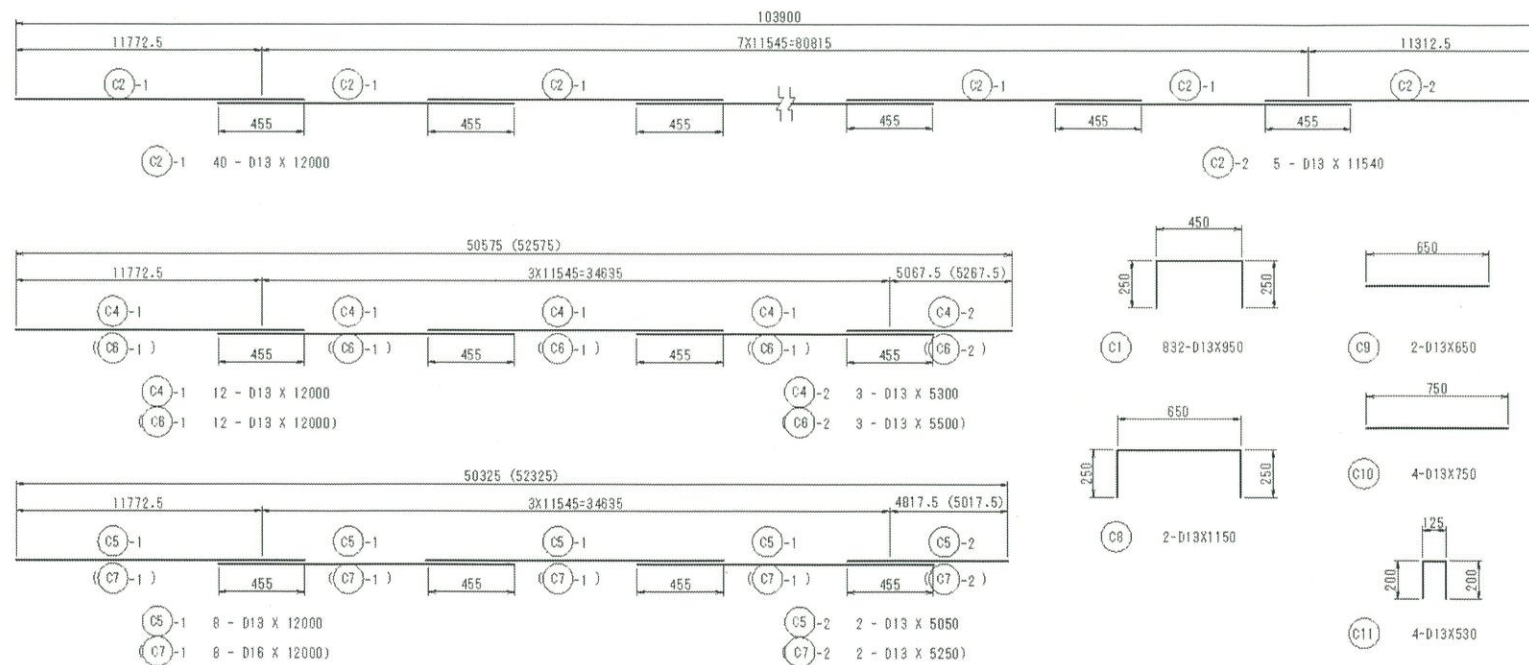


防護柵補強鉄筋図

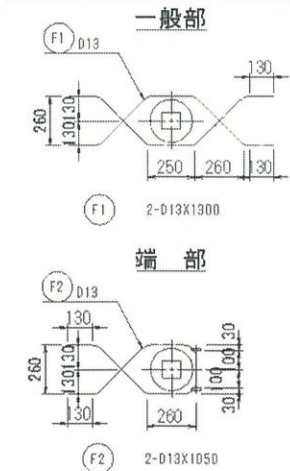

鉄 筋 表

記 号	径	長さ (mm)	本数	単位質量	1本当り質量	質量 (kg)	備 考
C-1	D13	950	832	0.995	0.95	790	
C2-1	D13	12000	40	0.995	11.94	478	
C2-2	D13	11540	5	0.995	11.48	57	
C4-1	D13	12000	12	0.995	11.94	143	
C4-2	D13	5300	3	0.995	5.27	16	
C5-1	D13	12000	8	0.995	11.94	96	
C5-2	D13	5050	2	0.995	5.02	10	
C6-1	D13	12000	12	0.995	11.94	143	
C6-2	D13	5500	3	0.995	5.47	16	
C7-1	D13	12000	8	0.995	11.94	96	
C7-2	D13	5250	2	0.995	5.22	10	
C8	D13	1150	2	0.995	1.14	2	
C9	D13	650	2	0.995	0.65	1	
C10	D13	750	4	0.995	0.75	3	
C11	D13	530	4	0.995	0.53	2	
F1	D13	1300	208	0.995	1.29	268	
F2	D13	1050	8	0.995	1.04	8	
						D13	2139 kg (SD295A)
						計	2139 kg

日 付

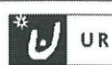

都市機構 東京都心支社

部 長

次 長

チーフリーダー

担 当

設計事務所

大日本コンサルタント (株)

工事名称

設計名称

新田豊島橋 (仮称) 実施設計

図面名称

地 覆 配 筋 図 (参考図)

縮 尺

図 示

図面番号

J-104