
共通詳細図（その３）S=1:10


作業用マンホール詳細

アーチリブ腹板センター部
（製作数=2）

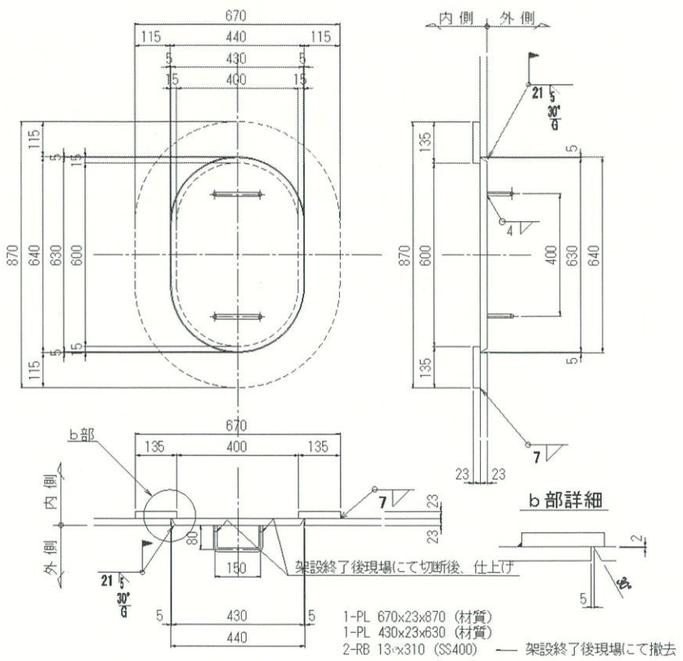


b部詳細

補剛桁の端ダイヤフラム部
（製作数=4）

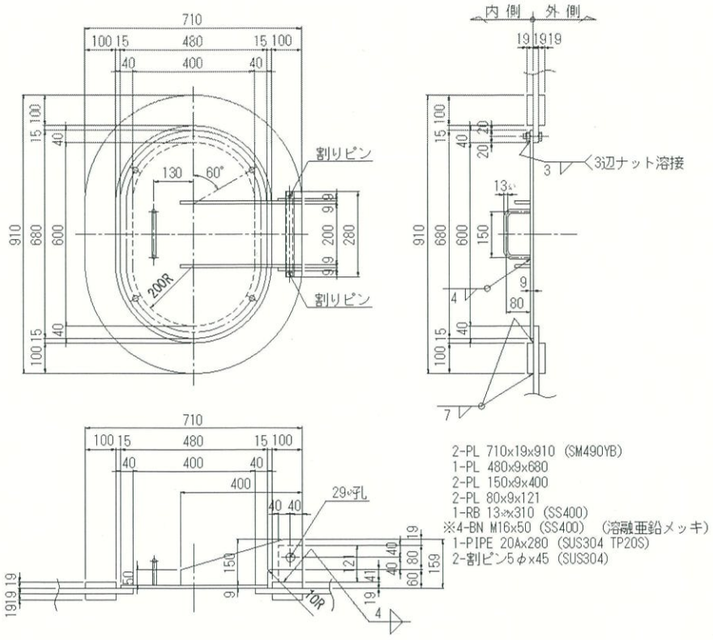


ハンドホール詳細

アーチリブ・補剛桁腹板部

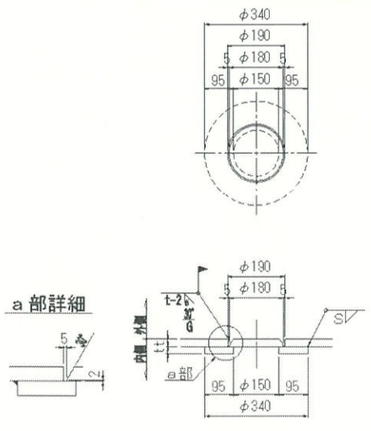

デッキ部

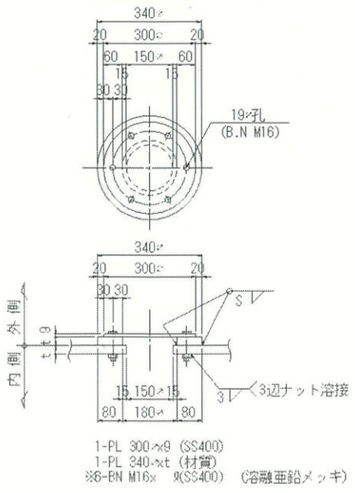

		t	S	材質	員数
アーチリブ腹板部	JU1,JU2,JU7,JU8部	23	7	SM570TMC	8
	JU3,JU4,JU5,JU6部	23	7	SM490YB	8
	J3,J14部	23	7	SM570TMC	4
補剛桁腹板部	J1,J16,JE1,JE2部	18	6	SM490YB	8

		t	R	S	材質	員数	
車道のデッキプレート部	J2,J3,J14,J15部	12	55	6	SM490YA	12	←3個×4箇所
	J5,J7,J8,J9,J10,J12部	〃	〃	〃	〃	30	←5個×6箇所
	J6,J11部	〃	〃	〃	〃	4	←2個×2箇所
歩道のデッキプレート部	J1,J3,J5,J7,J8,J9 J10,J12,J14,J16部	10	50	6	SM400A	20	←2個×10箇所

注）
1．特記なき材質は全てSM400Aとする。
2．特記なきスカーラップは全て35Rとする。
3．✦印はトルシア形高力ボルトM22（S10T）を示す。
4．添架物の取付寸法及び補強板詳細は別図を参照のこと。
5．※印は、溶融亜鉛メッキを施す。

日付	都市機構 東京都心支社	部長 次長 チームリーダー 担当	設計事務所	工事名称	設計名称	図面名称	縮尺	図面番号
			大日本コンサルタント（株）		新田豊島橋（仮称）実施設計	共通詳細図（その３）	図示	J-12