


"A"部詳細 S=1:10


アーチリブ (その9-1) S=1:30

面取り処理図 S=1:10

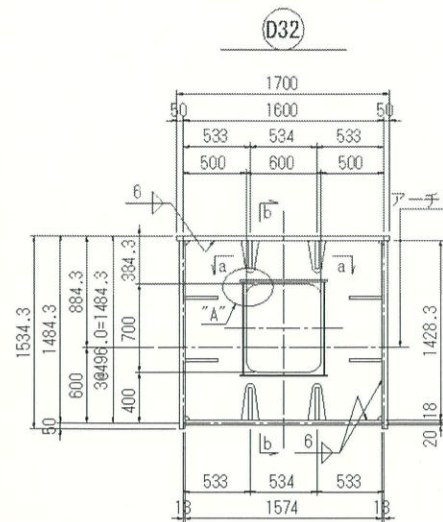


1-D1A PL 1574x9x1428
4-PL 100x10x700
4-PL 90x10x740

a-a

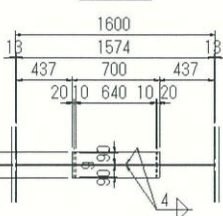


E-E

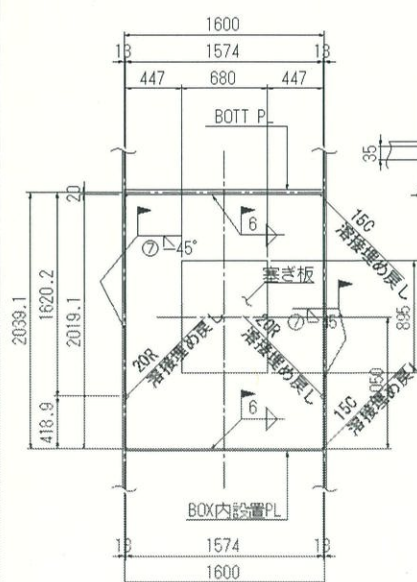


1- PL 1574x9x2019
1- PL 740x 9x995...点検用扉図参照
2- PL 45x 9x740...点検用扉図参照
2- PL 45x 9x955...点検用扉図参照

- 注)
1. 特記なき材質は全てSM400Aとする。
 2. 特記なきスカーラップは全て35Rとする。
 3. +印はトルシア形高力ボルトM22 (S10T) を示す。
 4. A-A, B-B, F-F, G-G, H-H, 部断面はアーチリブ (その9-2) 図を参照のこと。
 5. C-C, D-D, 縦リブ断面はアーチリブ (その9-3) 図を参照のこと。
 6. ダイアフラム断面、横リブ断面はアーチリブ (その9-4) 図を参照のこと。
 7. マンホール詳細は、アーチリブ (その9-2) "b" を参照のこと。
 8. 隅角部の梯子詳細は、別紙参照のこと。


補助照明取付詳細 S=1:10

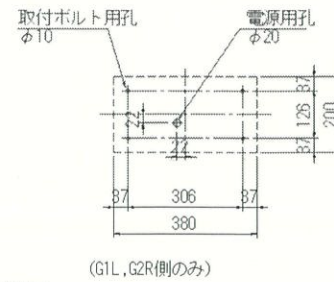


スカーラップ詳細図

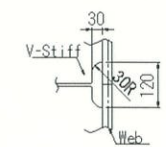


配置図 S=1:300

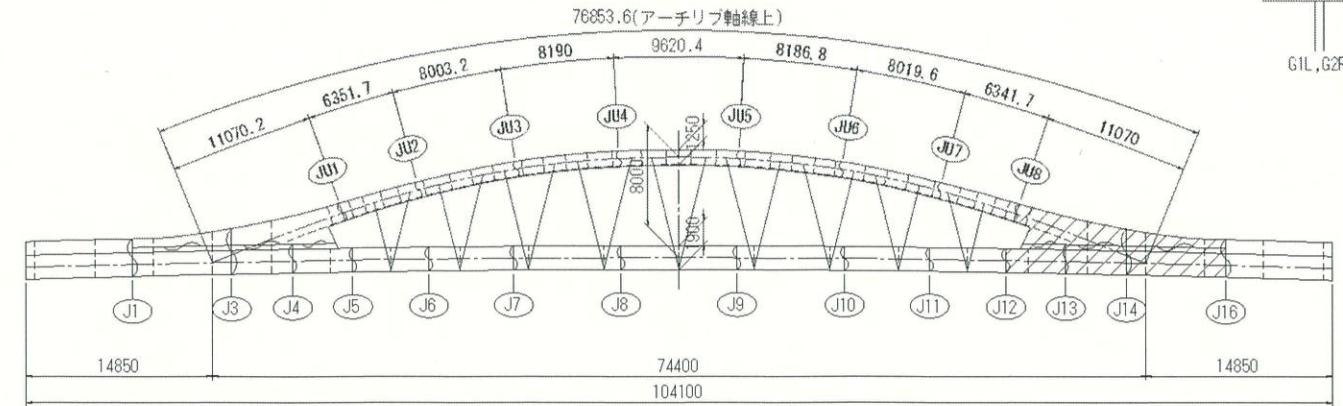

安定器箱固定板 S=1:10

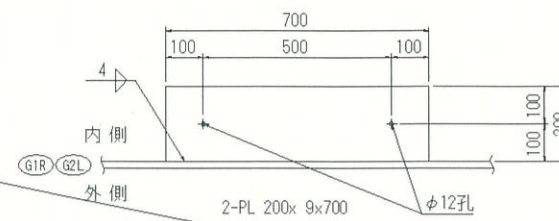

- 1 2-WEB PL 3138x23x9039 (SM570TMC)
- 2 2-WEB PL 1292x23x7983 (SM570TMC)
- 3 2-WEB PL 2291x23x4784 (SM570TMC)
- 4 2-WEB PL 2290x23x4897 (SM570TMC)
- 5 2-WEB PL 2289x23x8007 (SM570TMC)
- 6 2-RIB PL 230x25x959 (SM570TMC)
- 7 2-RIB PL 230x25x955 (SM570TMC)
- 8 2-RIB PL 230x25x2175 (SM570TMC)
- 9 2-RIB PL 230x25x2364 (SM570TMC)
- 10 2-RIB PL 230x25x2221 (SM570TMC)
- 11 2-RIB PL 230x25x2250 (SM570TMC)
- 12 2-RIB PL 230x25x1758 (SM570TMC)
- 13 2-RIB PL 230x25x789 (SM570TMC)
- 14 2-RIB PL 230x25x1180 (SM570TMC)
- 15 2-RIB PL 230x25x561 (SM570TMC)
- 16 4-RIB PL 190x19x706 (SM490YB)
- 17 2-RIB PL 190x19x3612 (SM490YB)
- 18 2-RIB PL 190x19x1596 (SM490YB)
- 19 2-RIB PL 230x25x722 (SM570TMC)
- 20 2-RIB PL 230x25x947 (SM570TMC)
- 21 2-RIB PL 230x25x799 (SM570TMC)
- 22 2-RIB PL 230x25x910 (SM570TMC)
- 23 10-RIB PL 230x25x333 (SM570TMC)
- 24 2-RIB PL 230x25x544 (SM570TMC)

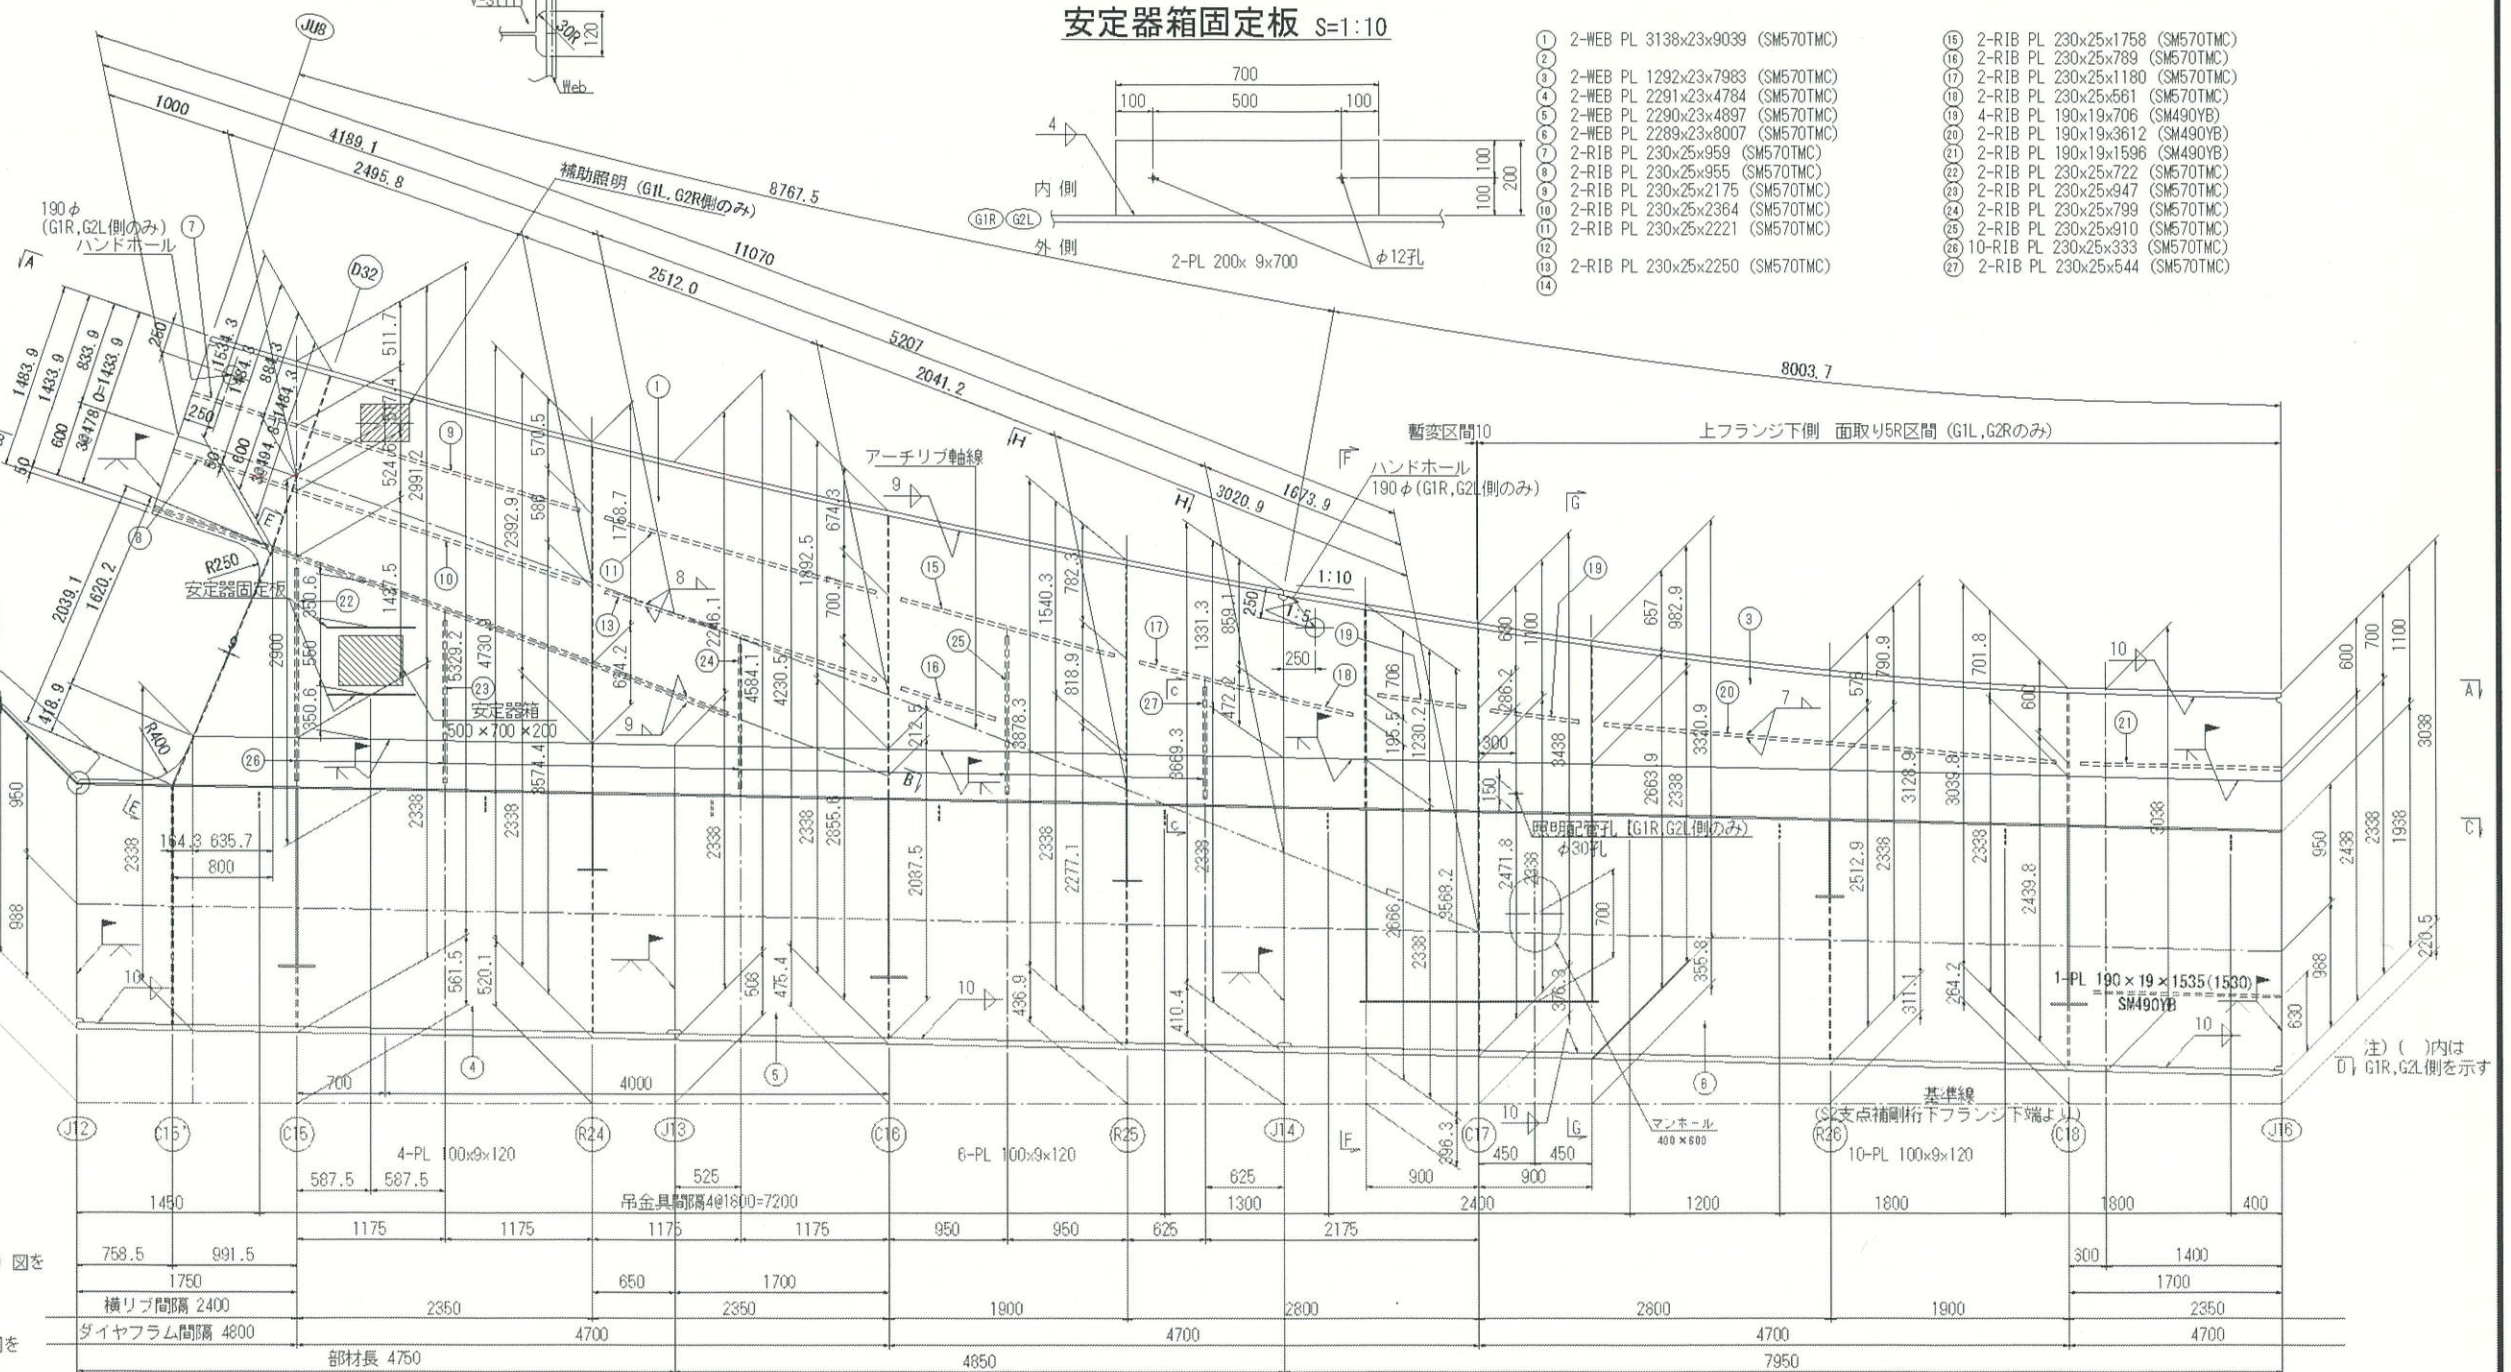

注) ()内は
D, G1R, G2L側を示す

日付

都市機構 東京都心支社

部長 次長 チームリーダー 担当

設計事務所
大日本コンサルタント (株)

工事名称
新田三丁目地区開発新田豊島橋 (仮称)
上部工建設工事 (第1回変更)

設計名称
新田豊島橋 (仮称) 実施設計

図面名称
アーチリブ (その9-1)

縮尺
図示
図面番号
J-50