

アーチリブ（その10-1）S=1:20

吊り材定着部詳細（その1）


C6-L 〈 C14-R 〉

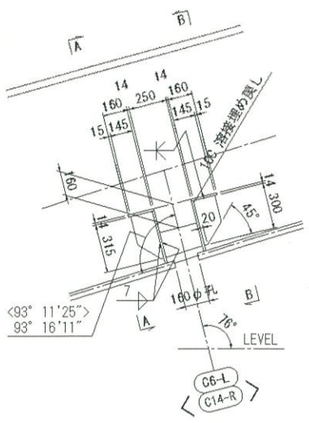

C6-R 〈 C14-L 〉

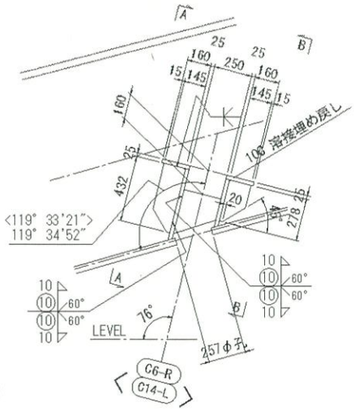


C7-L 〈 C13-R 〉

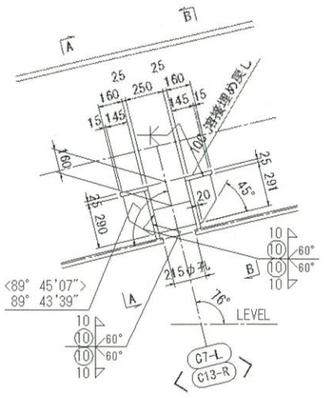


定着座金詳細 S=1:10

C6-L C14-R

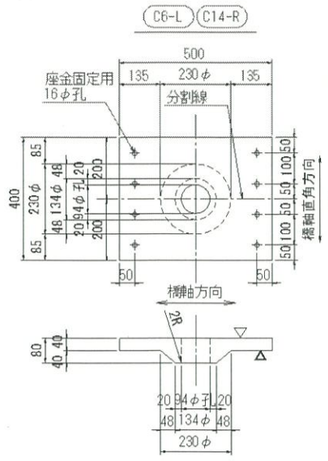


2-定着座金 500×80×200 (S45CN)

C6-R C7-L C13-R C14-L

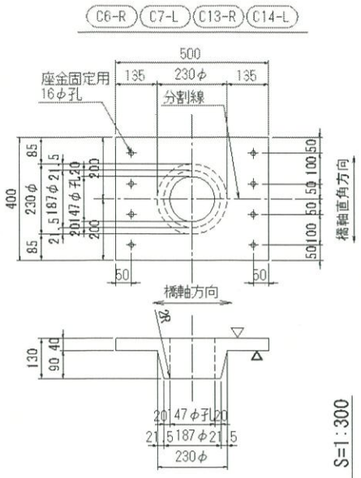


2-定着座金 500×130×200 (S45CN)


配置図 S=1:300

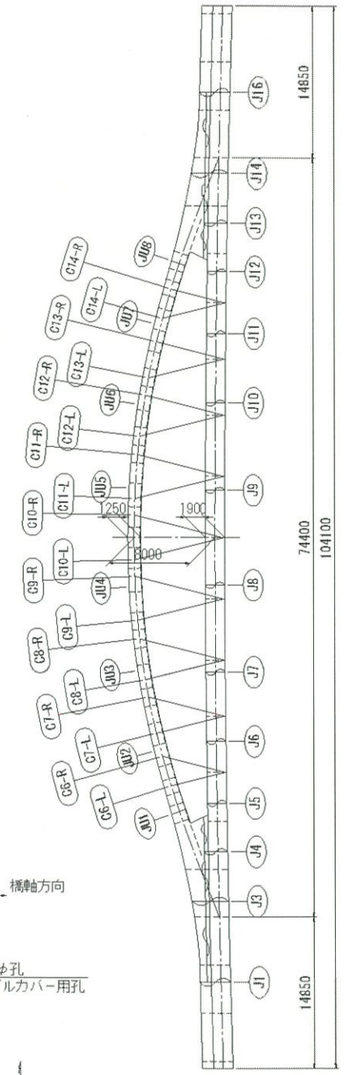


A-A〈B-B〉

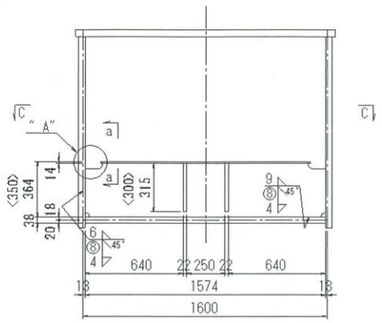


"A"部

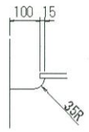


A-A〈B-B〉

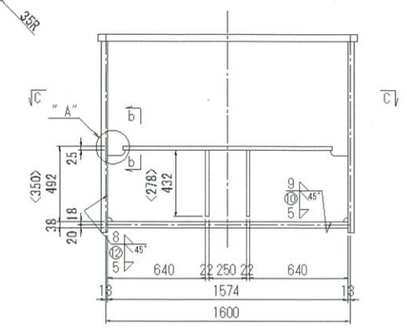

A-A〈B-B〉

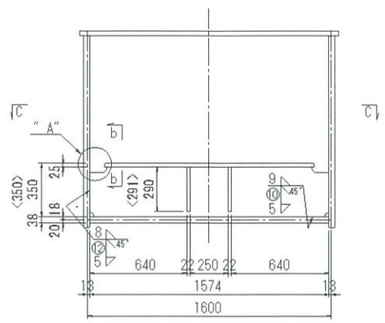


C-C

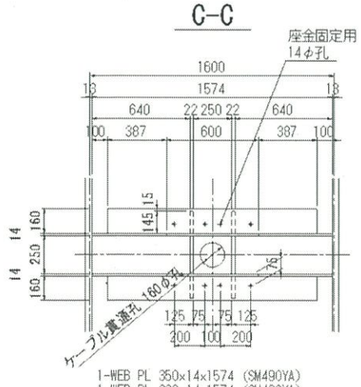


1-WEB PL 350×14×1574 (SM490YA)
1-WEB PL 336×14×1574 (SM490YA)
2-FLG PL 174×14×1374 (SM490YA)
2-RIB PL 145×22×315 (SM490YB)
2-RIB PL 145×22×300 (SM490YB)
2-RIB PL 250×22×167 (SM490YB)
＊4-BN M12×85(SS400)
(1種Nut ,3種Nut 2-W付)

C-C

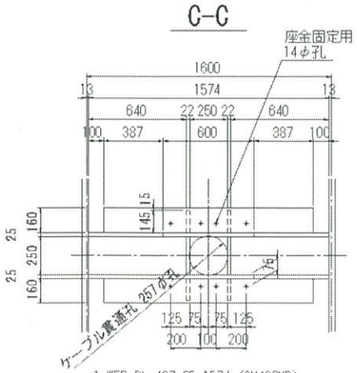

1-WEB PL 467×25×1574 (SM490YB)
1-WEB PL 325×25×1574 (SM490YB)
2-FLG PL 185×25×1374 (SM490YB)
2-RIB PL 145×22×432 (SM490YB)
2-RIB PL 145×22×278 (SM490YB)
2-RIB PL 250×22×300 (SM490YB)
＊4-BN M12×95(SS400)
(1種Nut ,3種Nut 2-W付)


C-C

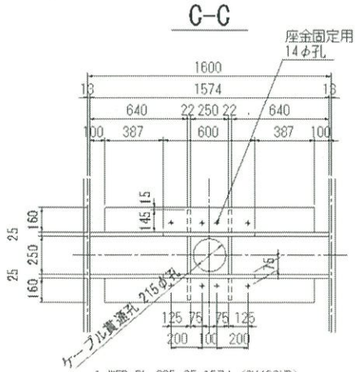


1-WEB PL 325×25×1574 (SM490YB)
1-WEB PL 326×25×1574 (SM490YB)
2-FLG PL 185×25×1374 (SM490YB)
2-RIB PL 145×22×290 (SM490YB)
2-RIB PL 145×22×291 (SM490YB)
2-RIB PL 250×22×165 (SM490YB)
＊4-BN M12×95(SS400)
(1種Nut ,3種Nut 2-W付)


吊材貫通孔部補強板詳細 S=1:10

C6-L C14-R 〈 C7-L C13-R 〉

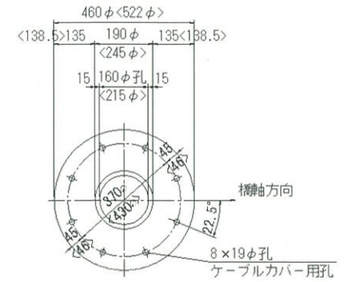


C6-R 〈 C14-L 〉

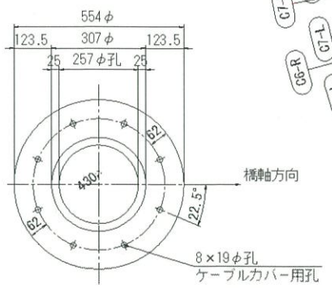

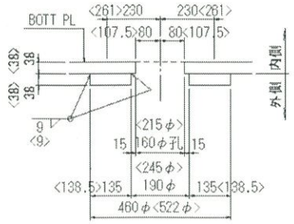


1-PL 460φ×38 (SM570TMC)
〈1-PL 522φ×38 (SM490YB)〉

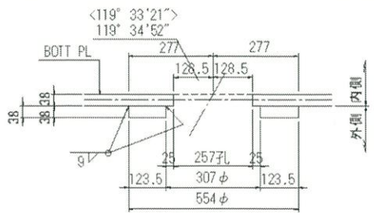


1-PL 554φ×38 (SM570TMC)

a-a

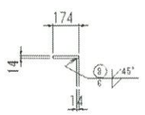

b-b

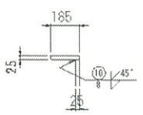

注）
1．特記なき材質は全てSM400Aとする。
2．特記なきスカーラップは全て35Rとする。
3．＋印はトルシア形高力ボルトM22（S10T）を示す。
4．各種詳細は共通詳細図を参照のこと。
5．＊印は溶接亜鉛メッキを施す。

日付	都市機構 東京都心支社	部長 次長 チームリーダー 担当	設計事務所	工事名称	設計名称	図面名称	縮尺	図面番号
	UR		大日本コンサルタント（株）	新田三丁目地区関連新田豊島橋（仮称）上部工整設工事（第1回変更）	新田豊島橋（仮称）実施設計	アーチリブ（その10-1）	図示	J-54