

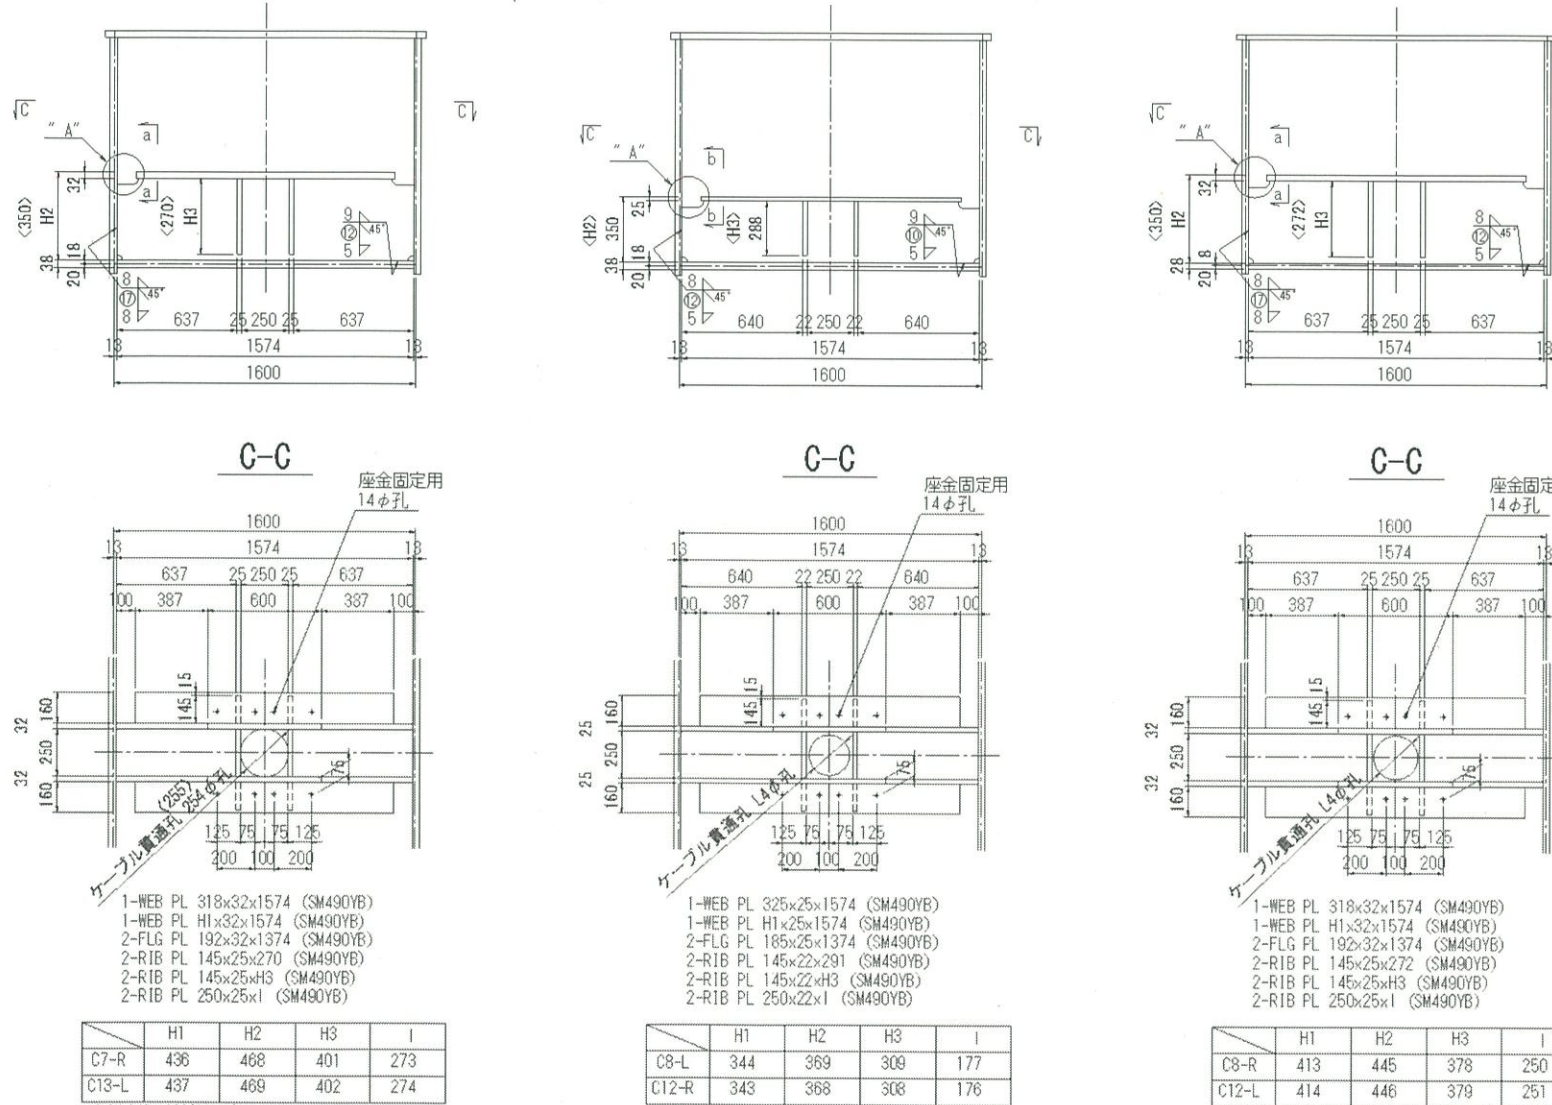


アーチリブ (その10-2) S=1:20


吊り材定着部詳細 (その2)

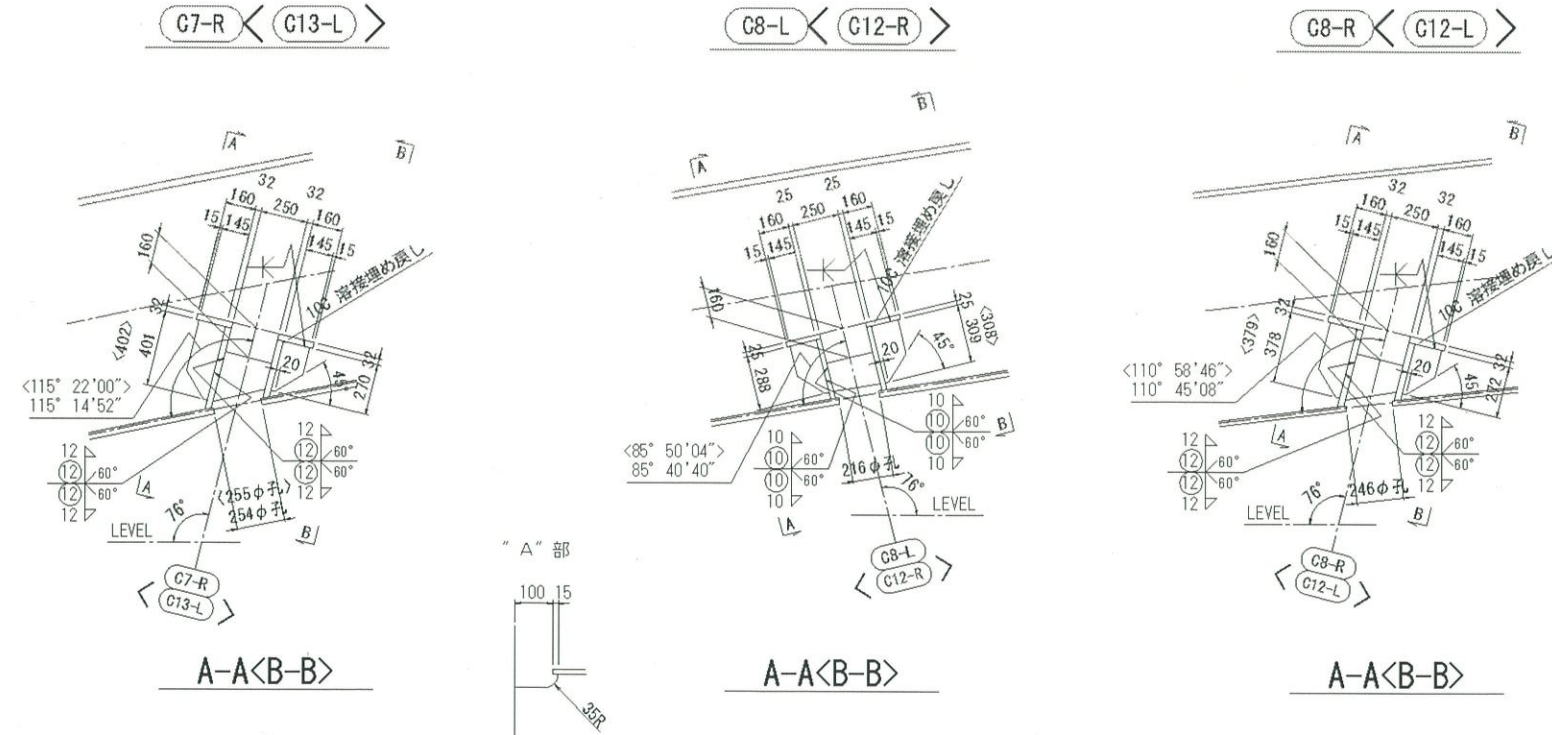



定着座金詳細 S=1:10

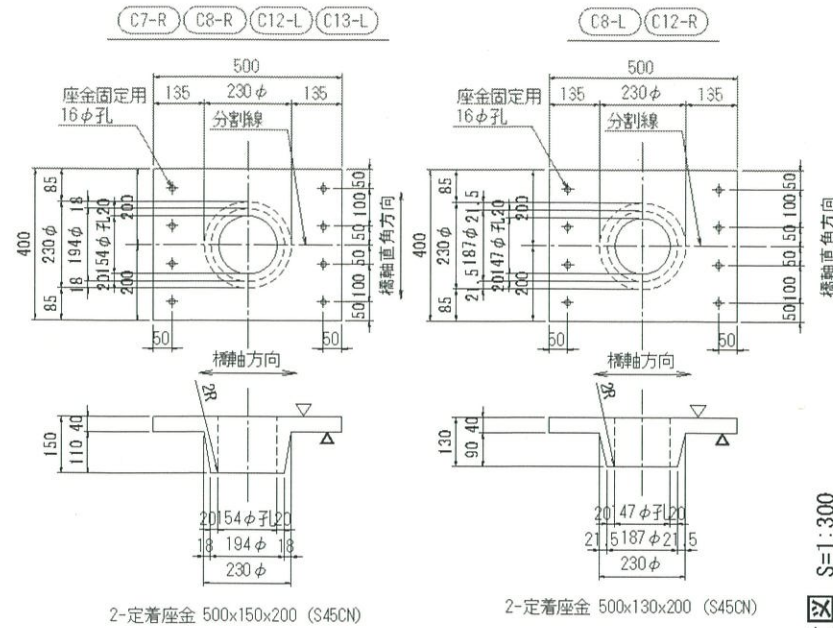

吊材貫通孔部補強板詳細 S=1:10

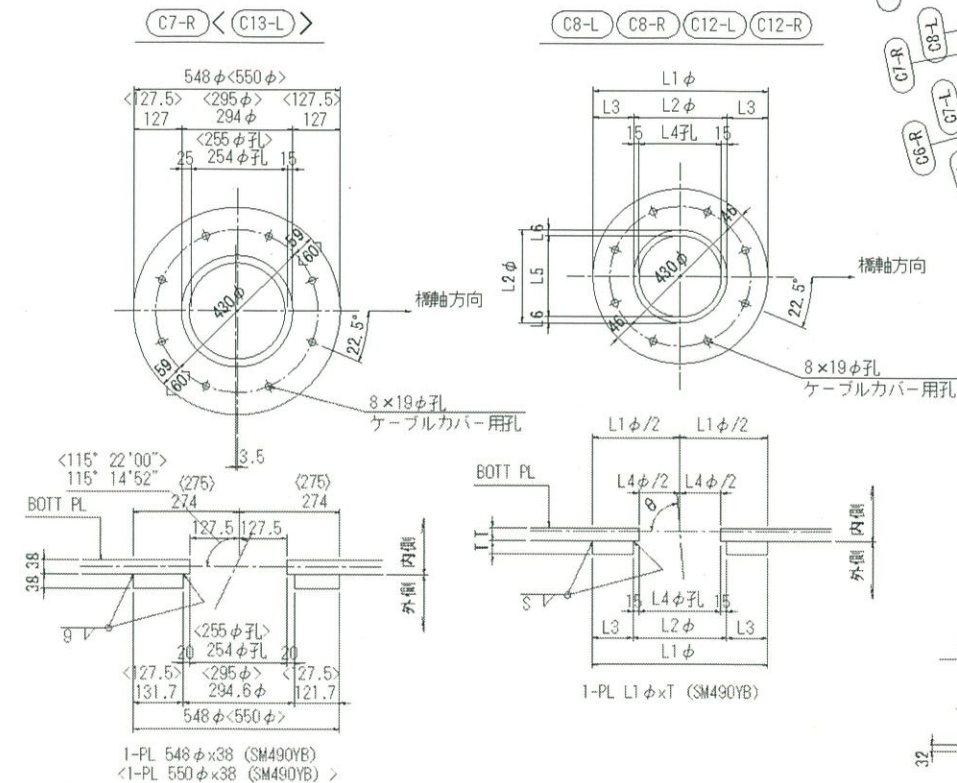

配置図 S=1:300

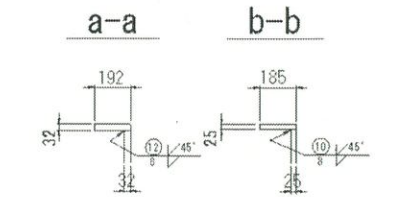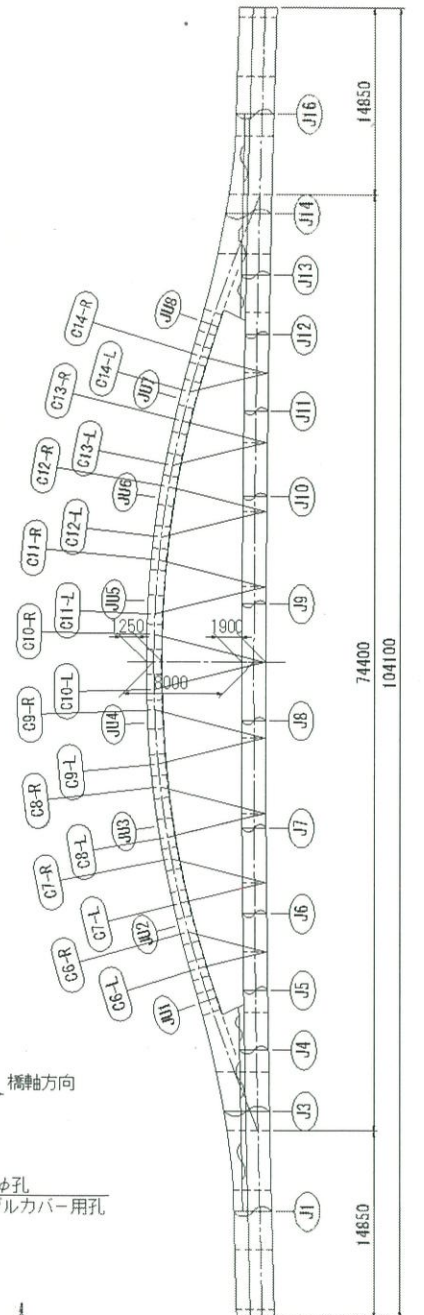

- 注)
1. 特記なき材質は全てSM400Aとする。
 2. 特記なきスカラーは全て35Rとする。
 3. +印はトルシア形高力ボルトM22 (S10T) を示す。
 4. 各種詳細は共通詳細図を参照のこと。
 5. *印は溶接垂鉛メッキを施す。