
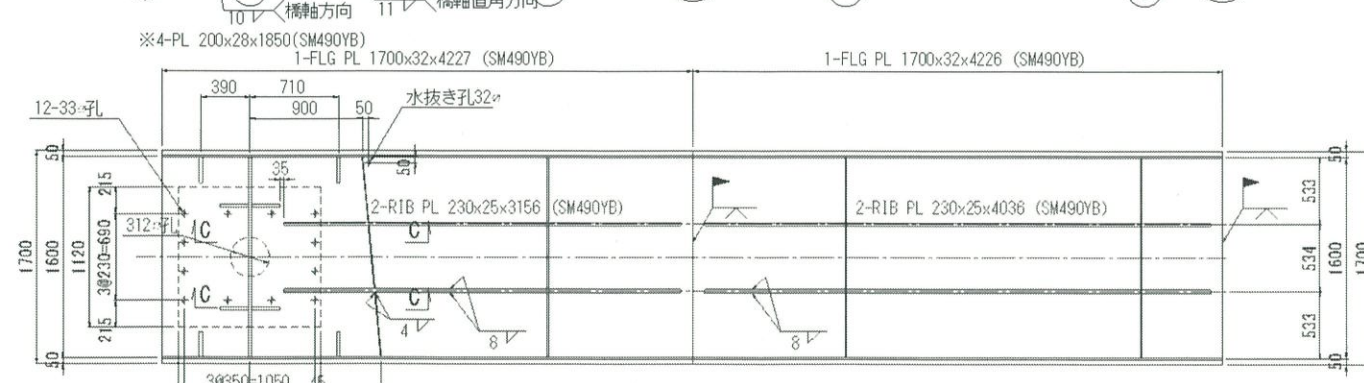


1-FLG PL 1700x16x1588 (SM490YA)


1-FLG PL 1700x30x3626 (SM490YB)

1-FLG PL 1700x30x4226 (SM490YB)

補剛桁 (その1-1) S=1:30

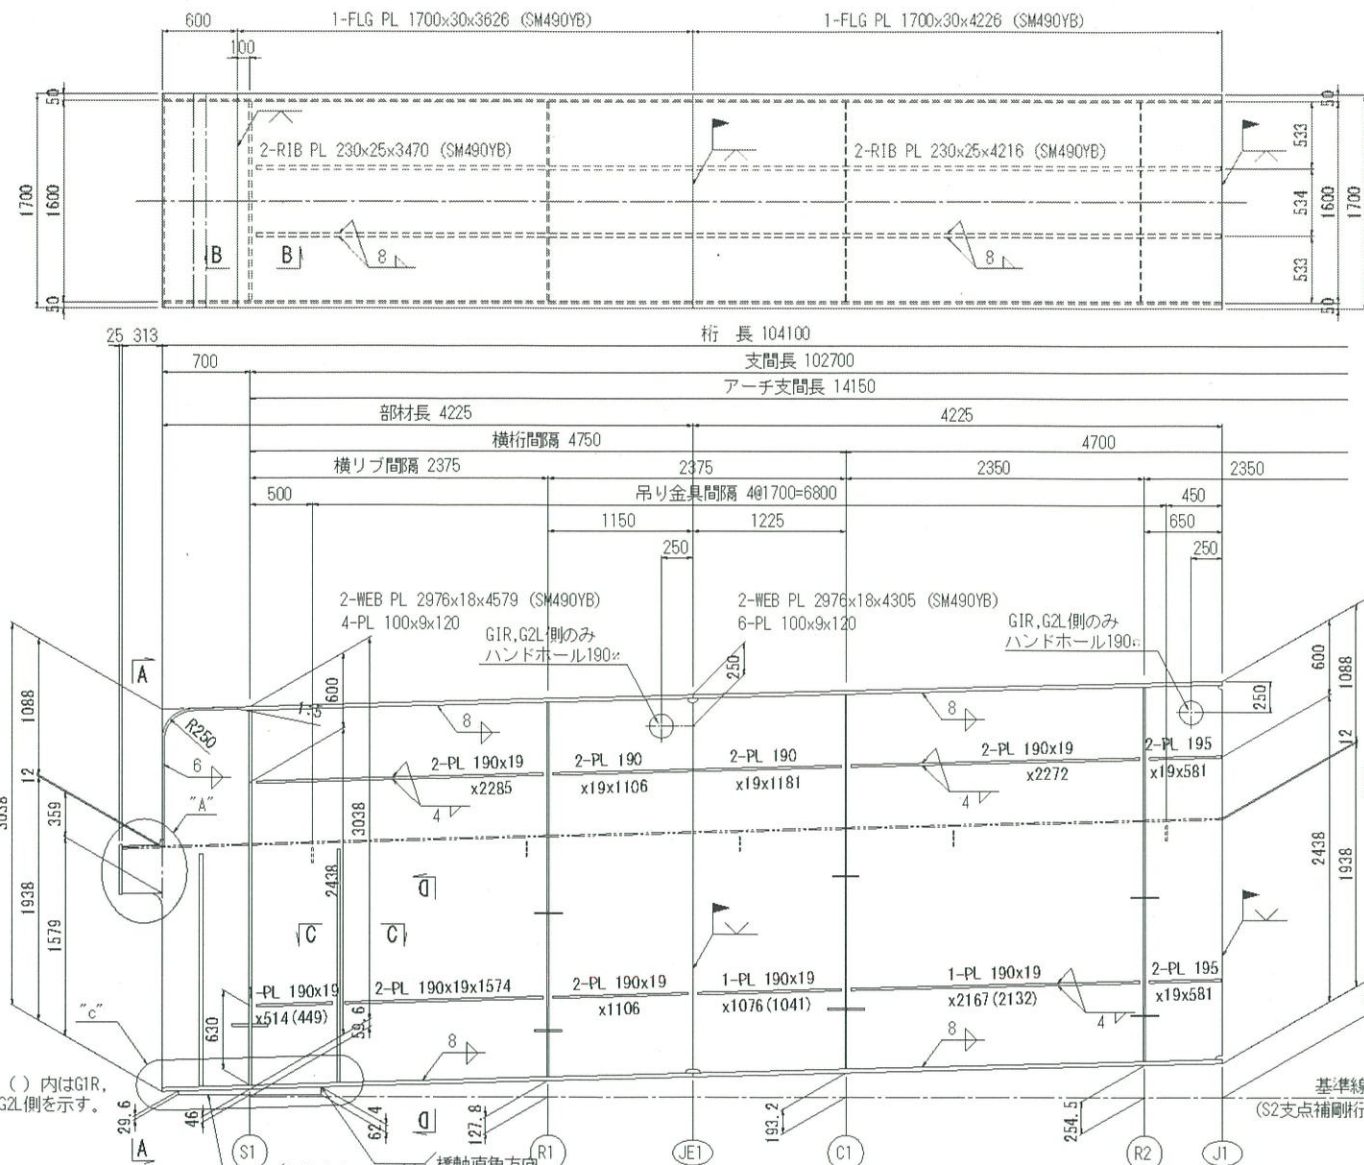


水抜き孔部詳細 S=1:5

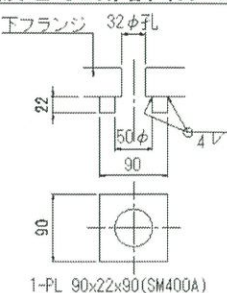



面取り処理図 S=1:10




吊り金具詳細 S=1:10

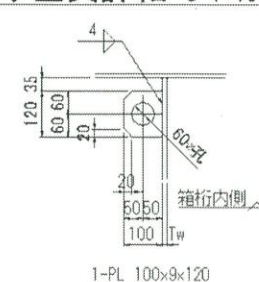


"B"部詳細 S=1:10

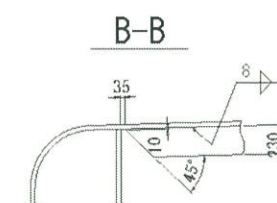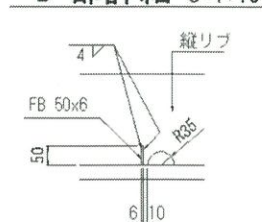



D-D

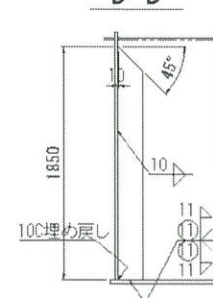


"c"部詳細

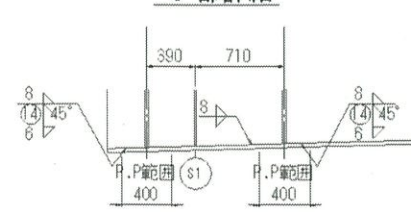


C-C

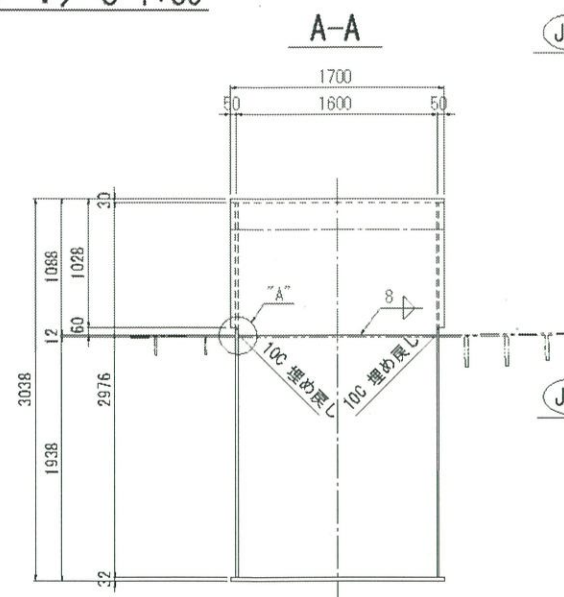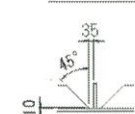

"A"部詳細 S=1:10

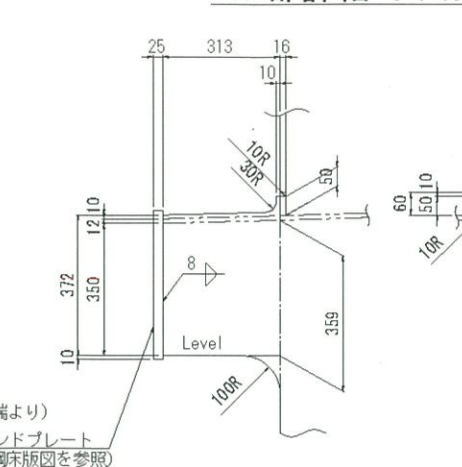


JE1 上フランジ側縦リブ添接

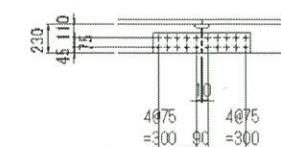


2-SPL PL 155x19x770 (SM490YB)
20-TCB M22x100 (S10T)

J1 上フランジ側縦リブ添接

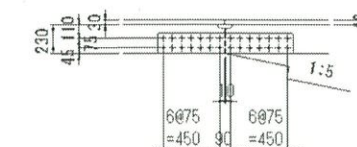

2-SPL PL 155x19x1070 (SM490YB)
28-TCB M22x100 (S10T)


JE1 下フランジ側縦リブ添接

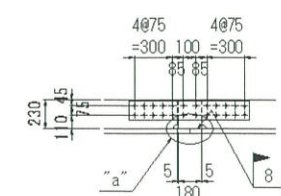

現場溶接の収縮を考慮してボルト孔を26.5φとする。

1-RIB PL 230x25x180 (SM490YB)
2-SPL PL 155x22x950 (SM490YB)
24-TCB M22x105 (S10T)


J1 下フランジ側縦リブ添接

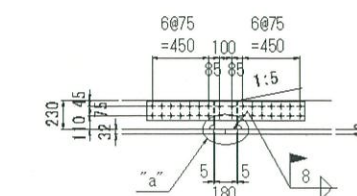

現場溶接の収縮を考慮してボルト孔を26.5φとする。


1-RIB PL 230x25x180 (SM490YB)
2-SPL PL 155x22x1250 (SM490YB)
32-TCB M22x105 (S10T)

JE1 J1 水平補剛材添接

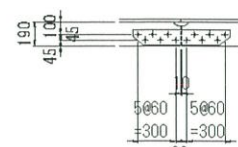


2-SPL PL 125x16x770 (SS400)
12-TCB M22x90 (S10T)
※ ボルト孔を全て26.5φとする。

配置図

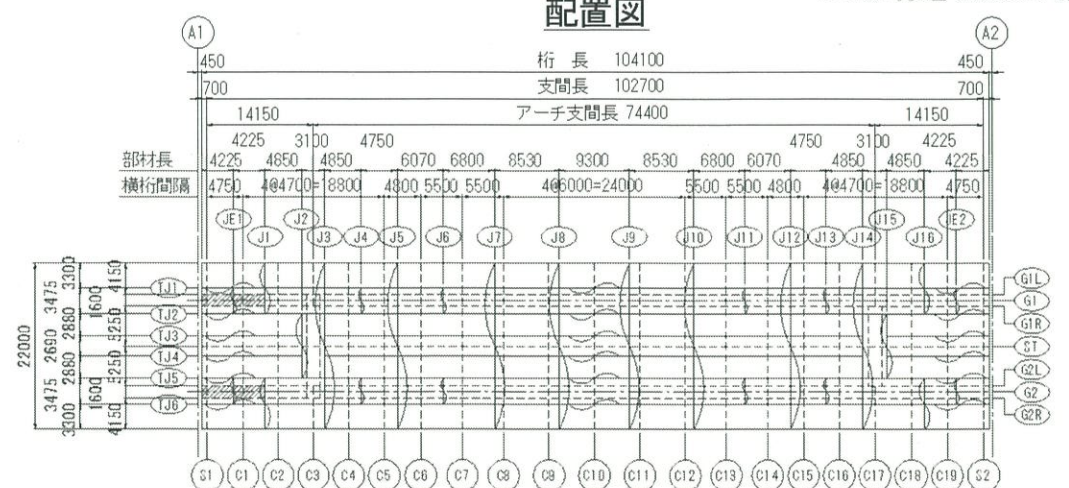

- 注)
1. 特記なき材質は全てSM400Aとする。
 2. 特記なきスカーップは全て35Rとする。
 3. S1, C1, R1, R2部断面図は補剛桁 (その1-2) 図を参照のこと。
 4. G1L, G2Rの上フランジ下側の面取りは5R処理とすること。

日付

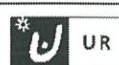

都市機構 東京都心支社

部長

次長

チームリーダー

担当

設計事務所

大日本コンサルタント (株)

工事名称

新田三丁目地区開発新田豊島橋 (仮称)
上部工建設工事 (第1圖表)

設計名称

新田豊島橋 (仮称) 実施設計

図面名称

補剛桁 (その1-1)

縮尺

図示

図面番号

J-57