

横 リ ブ S=1:30


R1 ～ R28 部

注） () 内はR11～R18を示す。

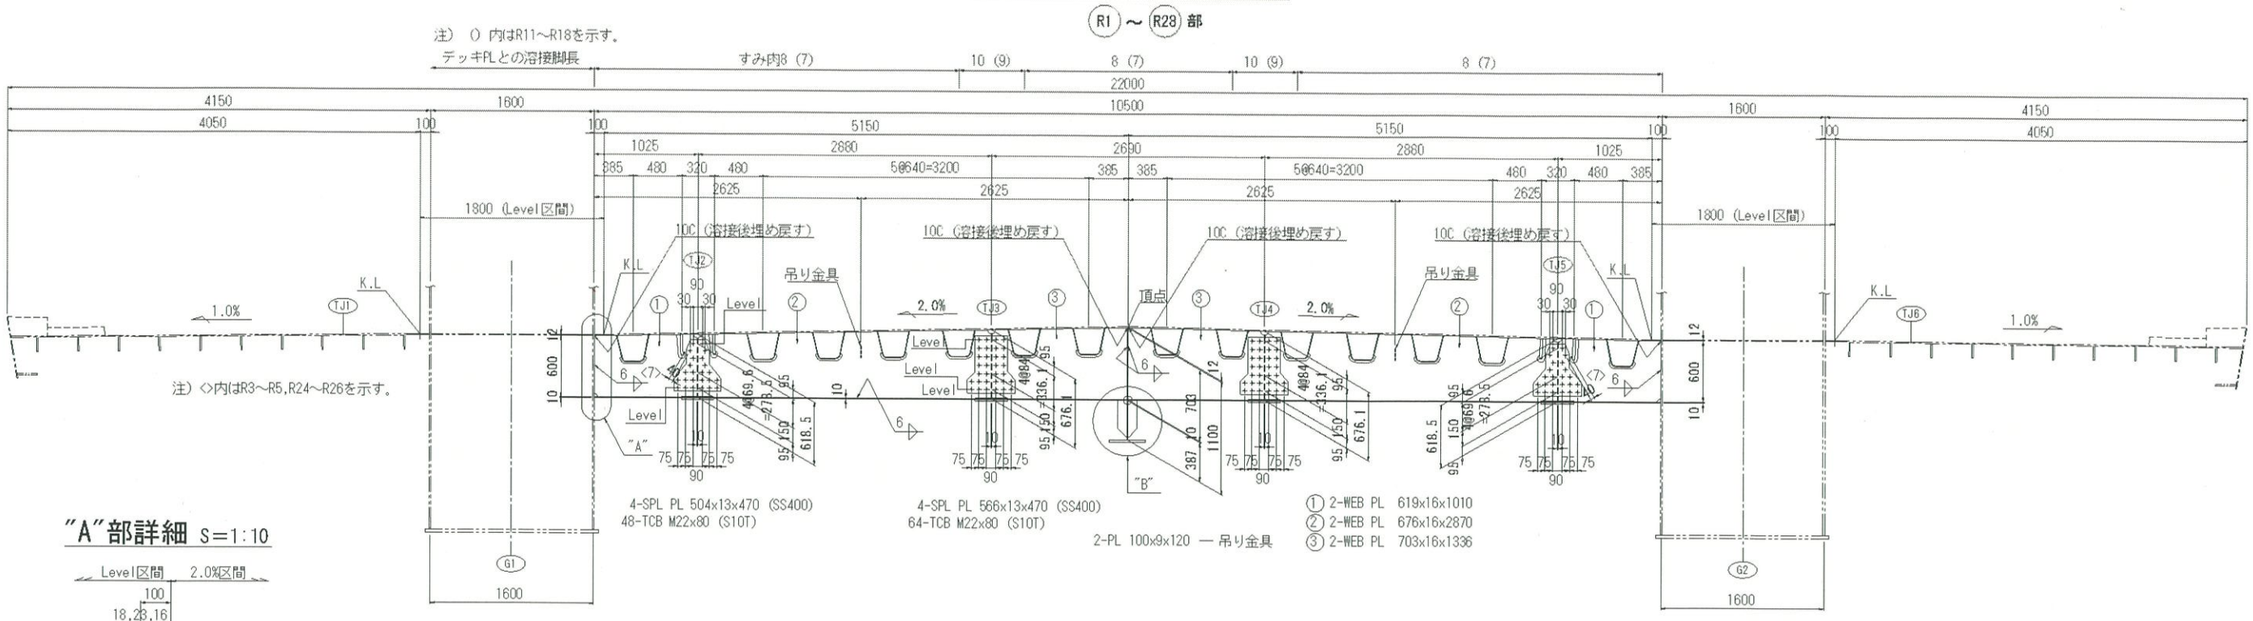


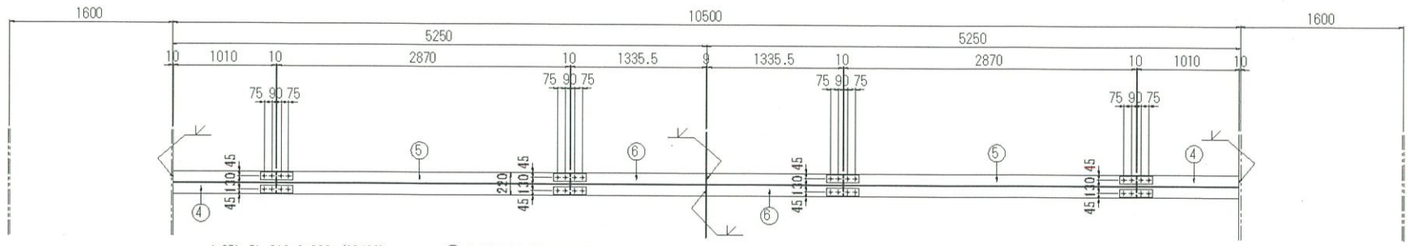


"A"部詳細 S=1:10

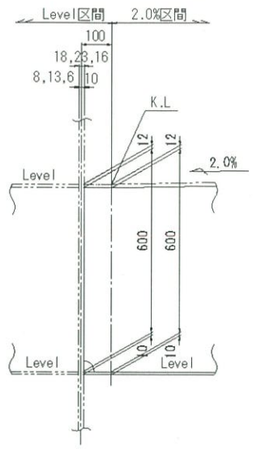


"B"部詳細 S=1:10

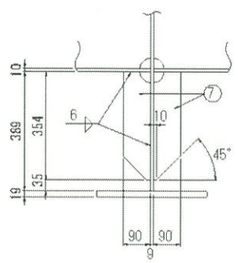

吊り金具詳細 S=1:10

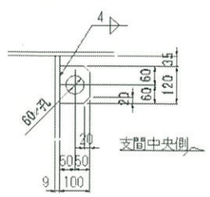

配 置 図

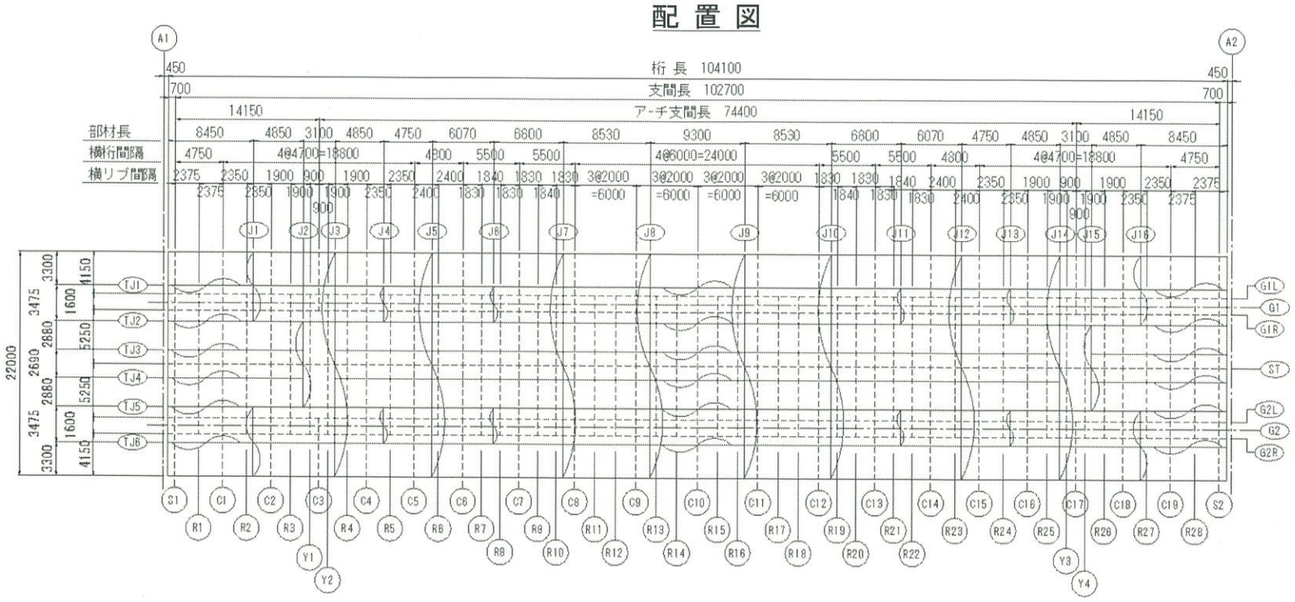

※ ボルト孔を全て26.5φとする。

注）
1．特記なき材質は全てSM400Aとする。
2．特記なきスカーラップは全て35Rとする。
3．✦ 印はトルシア形高力ボルトM22 (S10T) を示す。

日付	都市機構 東京都心支社	部長	次長	チームリーダー	担当	設計事務所	工事名称	設計名称	図面名称	縮尺	図面番号
	UR					大日本コンサルタント（株）	新田三丁目地区開通新田豊島橋（仮称）上部工建設工事（第1回変更）	新田豊島橋（仮称）実施設計	横リブ	図 示	J-76