



防護柵 (その1)

平面図 S=1/200

- 注記 1. 防護柵取付部の○印は支柱取付位置を示し、|印は橋梁継手部を示す。
2. 高欄取付部の○、●印はポスト取付位置を示し、○印はトップレール通し部を、●印は継手部を示す。
3. 高欄取付部の床版上の障害物（添接板等）を確認の上製作の事。

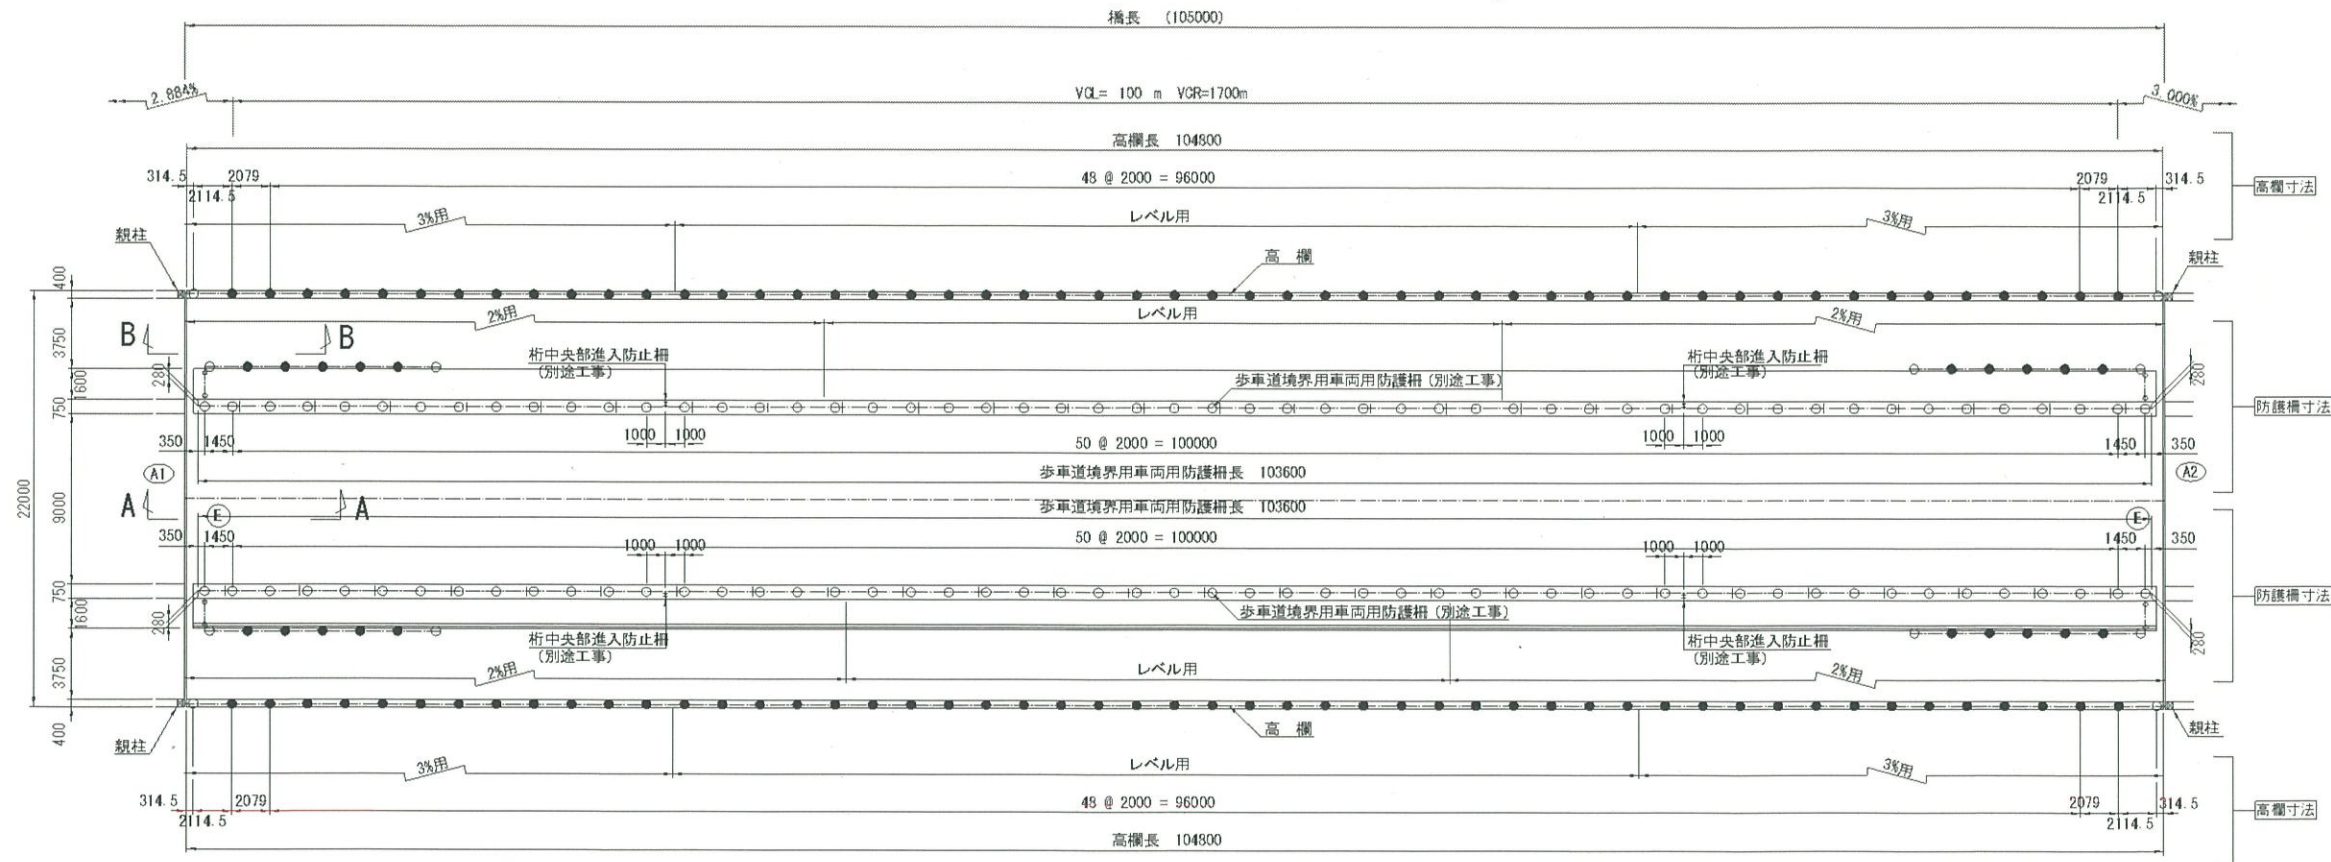

姿図 S=1/30

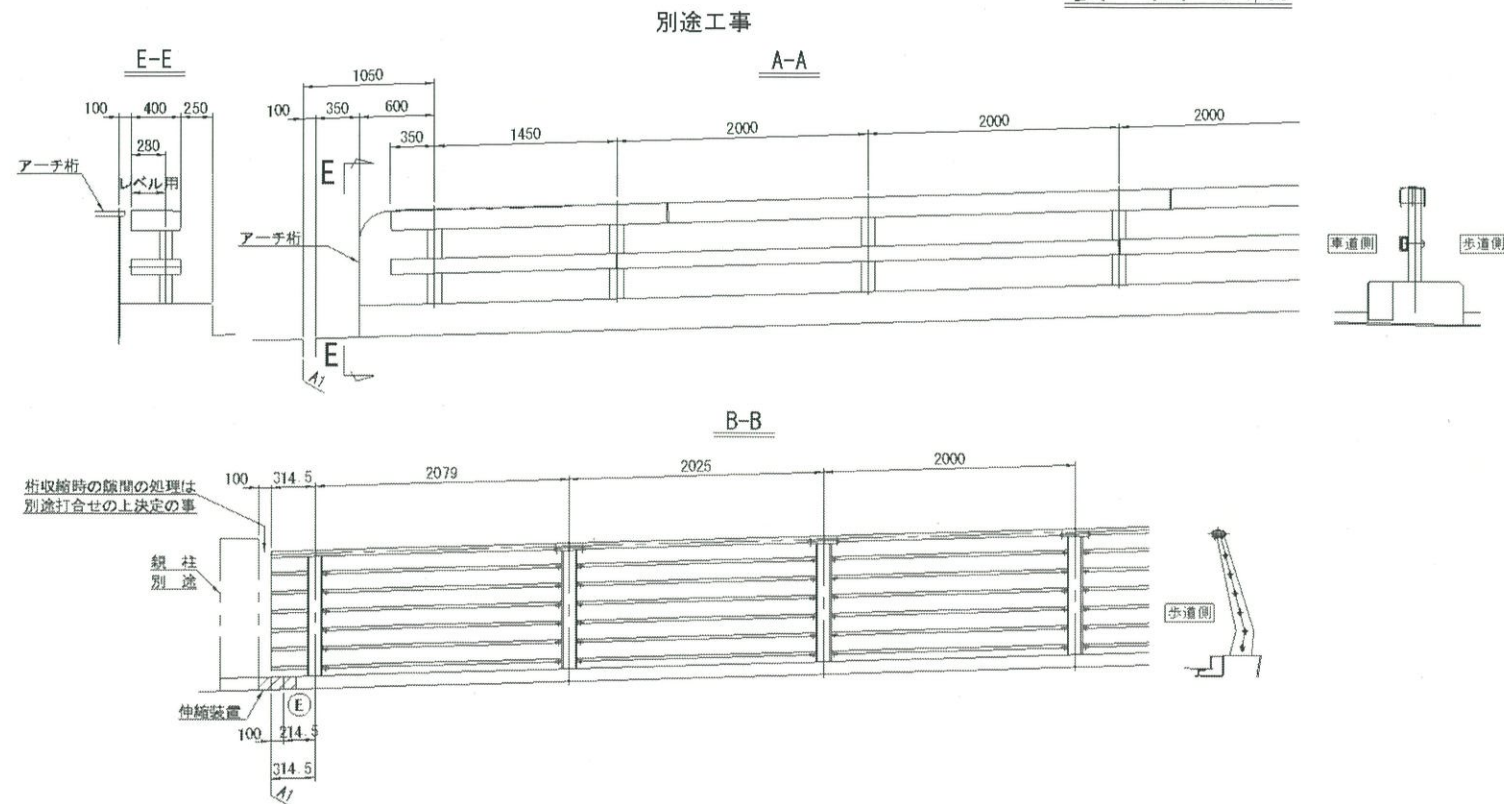

日付



都市機構 東京都心支社

部長

次長

チームリーダー

担当

設計事務所

大日本コンサルタント(株)

工事名称

新田三丁目地区開発新田豊島橋(仮称)
上部工建設工事(第1回変更)

設計名称

新田豊島橋(仮称)実施設計

図面名称

防護柵(その1)

縮尺

図示

図面番号

J-93