



A 1 橋台構造一般図(その3) S=1:50


正面図

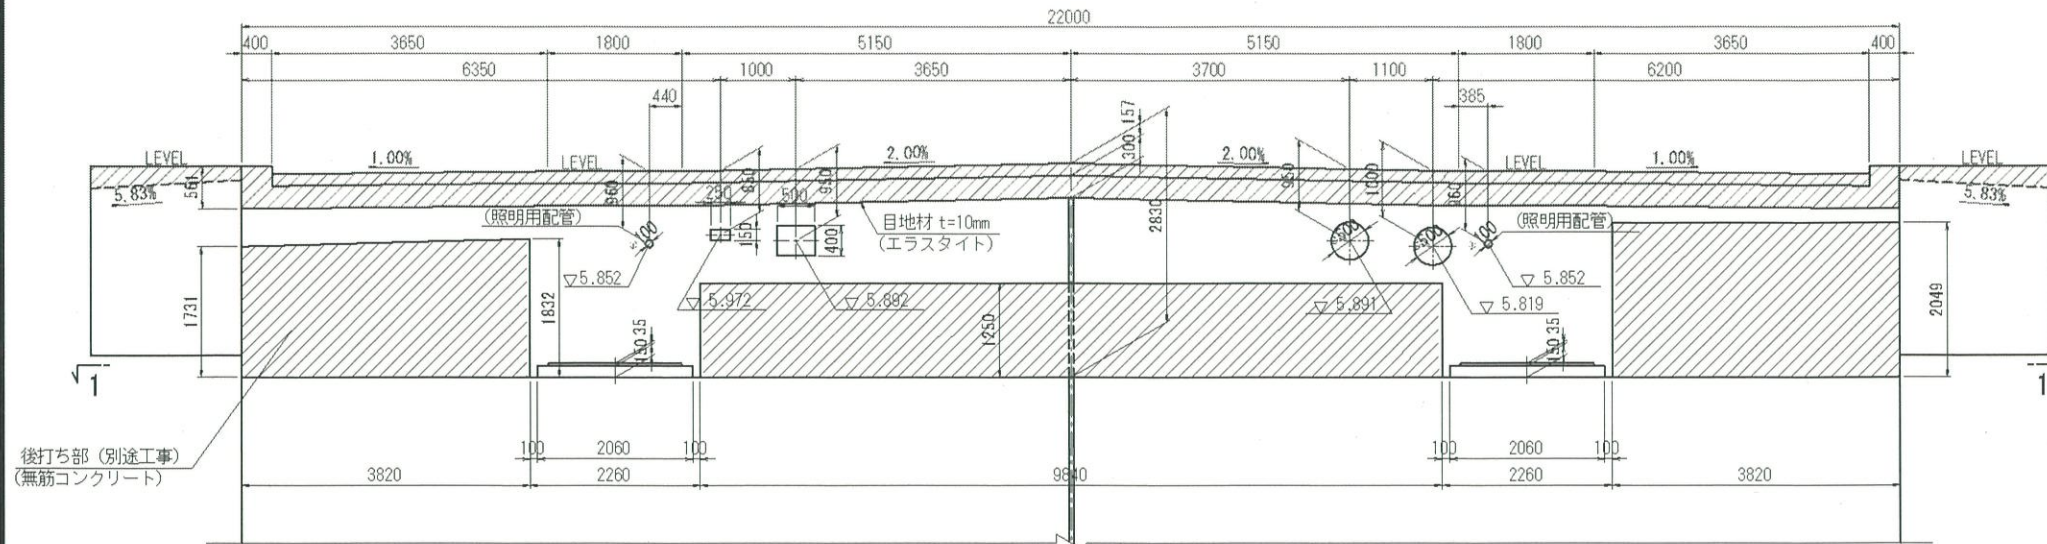


背面図

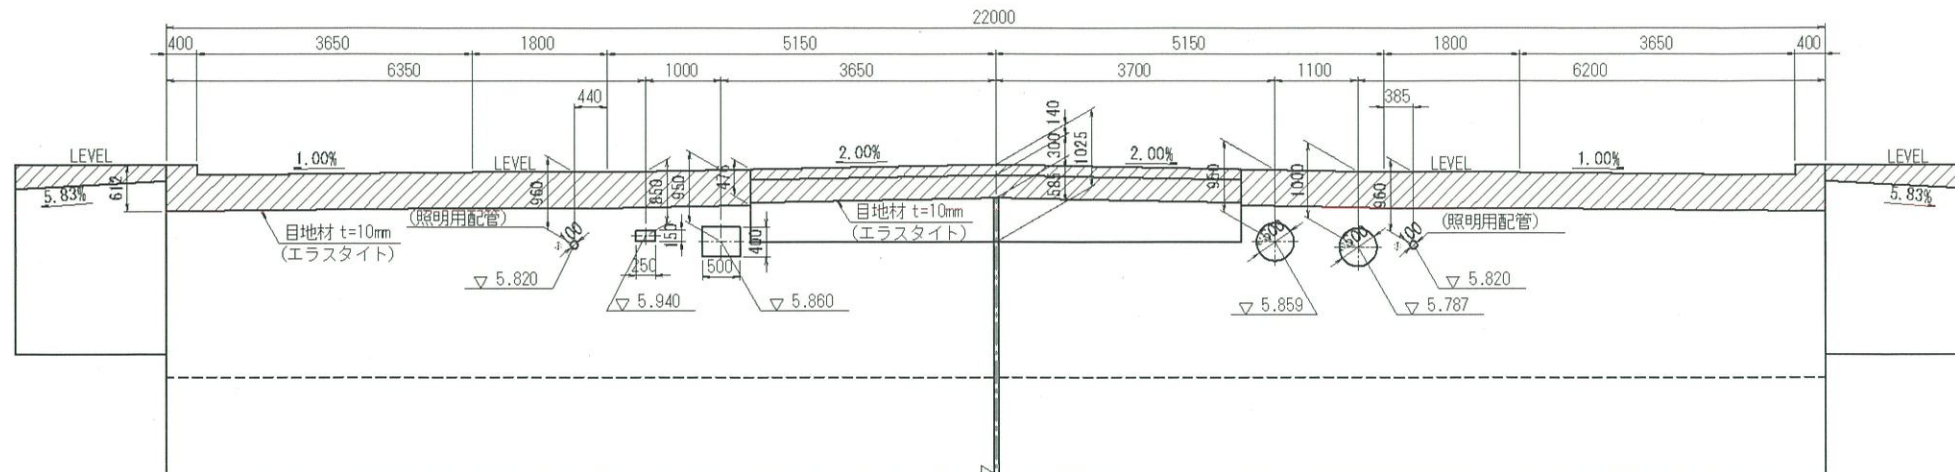

1-1

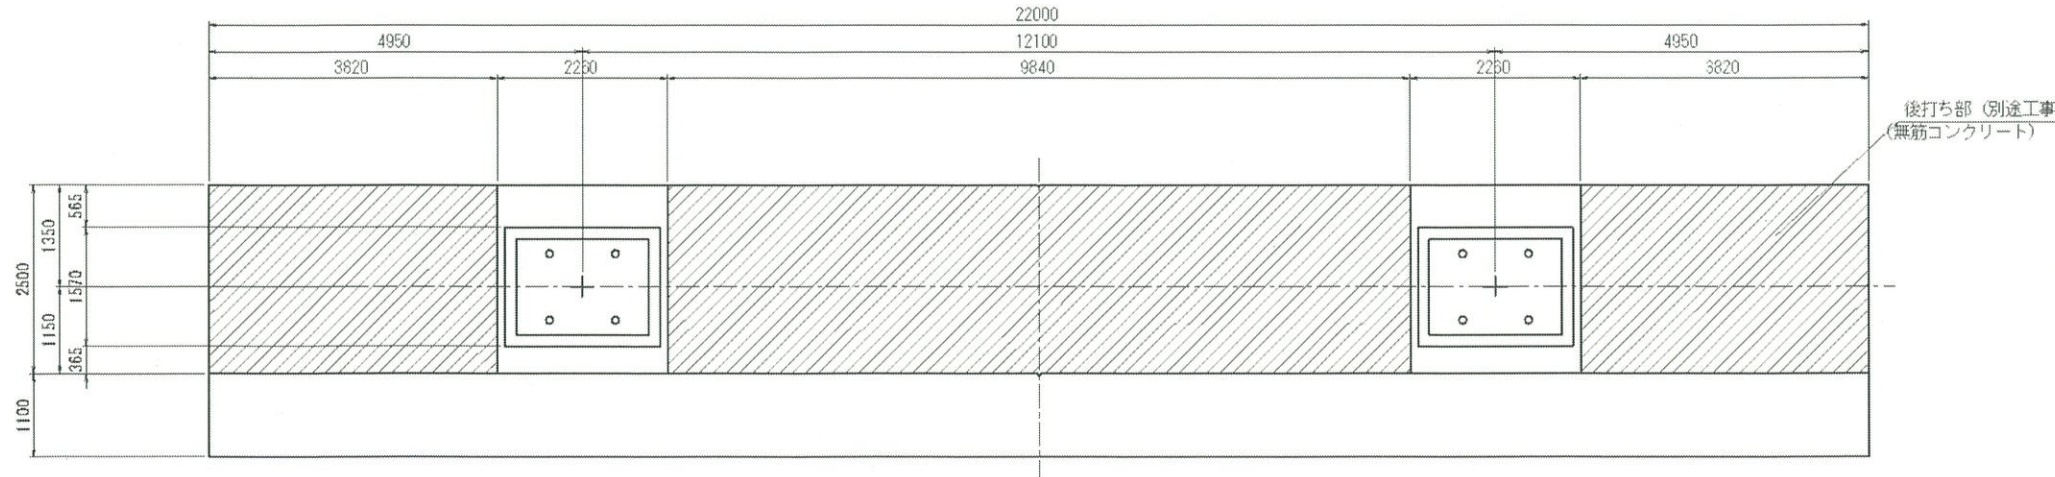


断面図

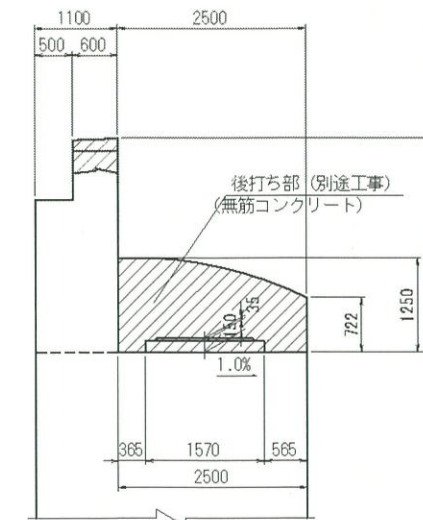

ノックオフ部詳細図 S=1:30


車道部

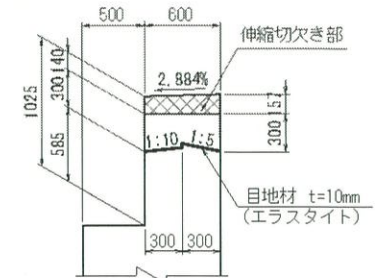


歩道部



支承箱抜き詳細図 S=1:30

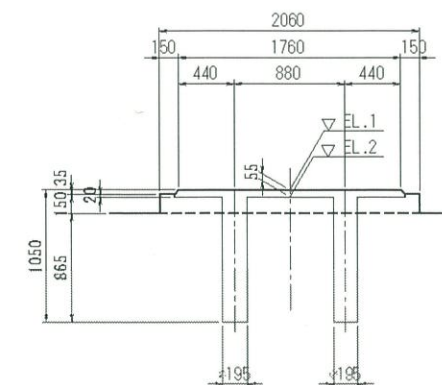

	G1	G2
EL.1	4.270	4.270
EL.2	4.215	4.215
モルタル厚	35	35
台座高	150	150
下部工天端高	4.085	4.085

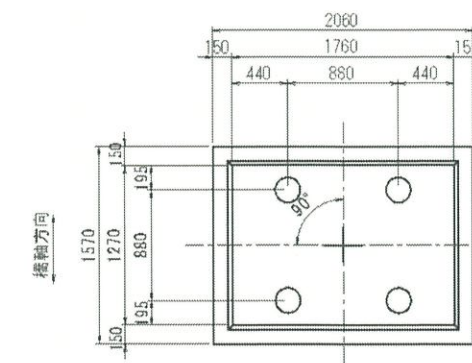

部は 後打ち部 (別途工事) を示す。