




鋼管杭 S=1:50

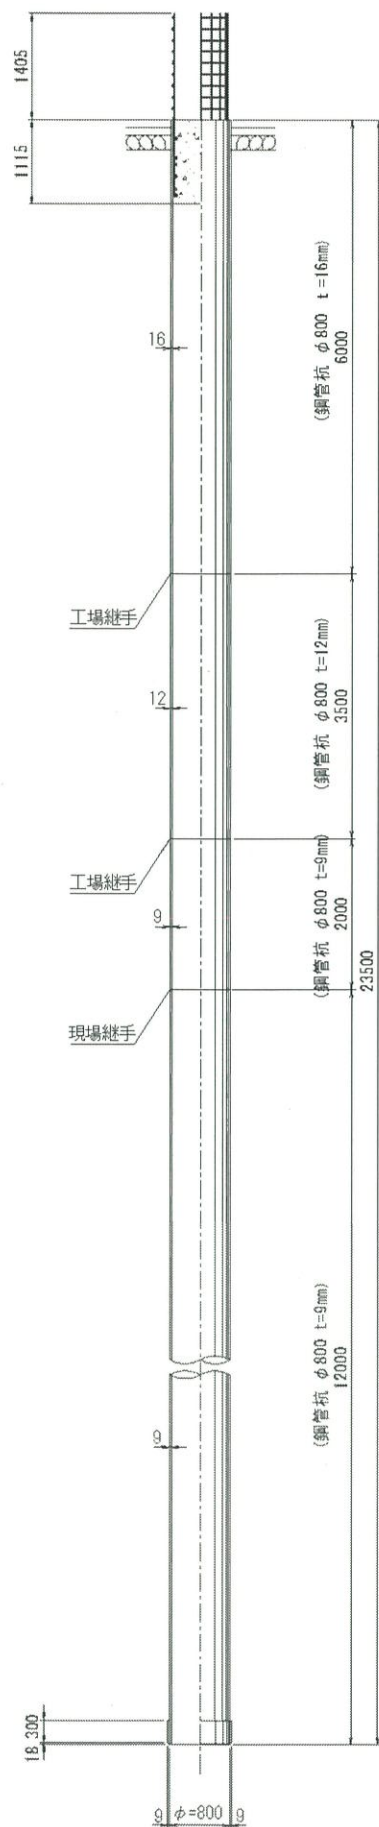


杭頭部詳細図

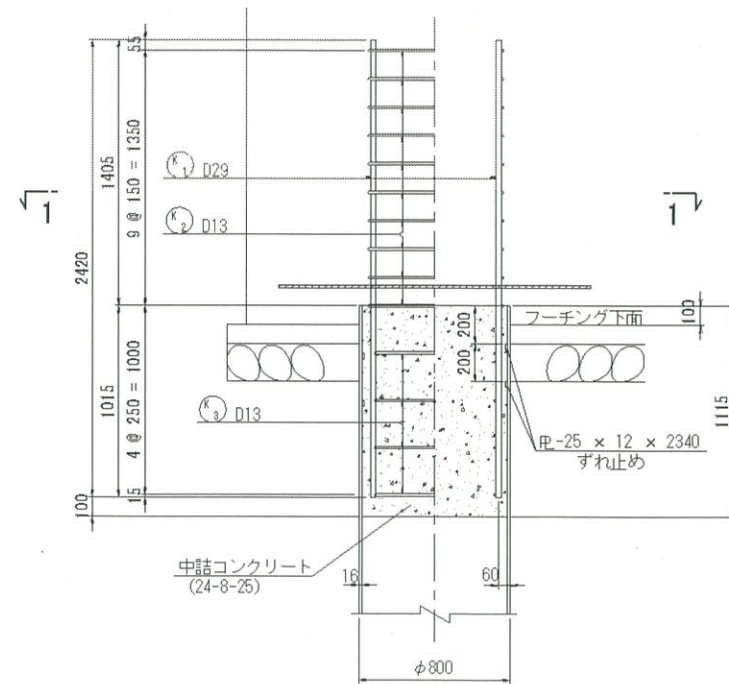

現場溶接ずれ止め詳細図

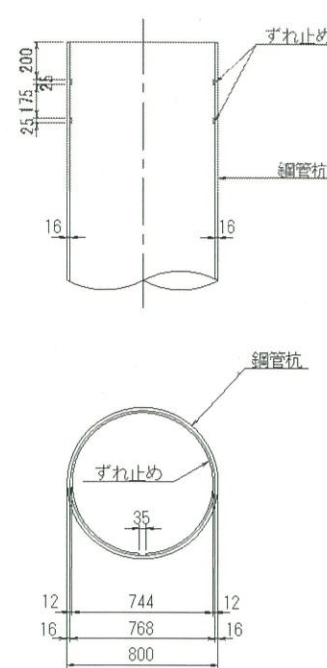


工場継手詳細図 S=1:2

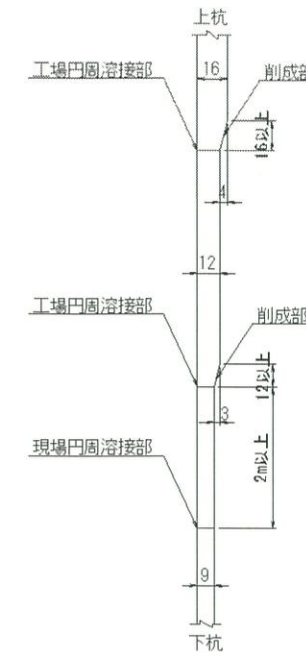


材料表

種別	断面寸法	長さ(mm)	本数	単位質量(kgf/m)	本当り質量(kg)	質量(kg)	摘要
(kgf/m)							
鋼管杭	φ800×16	6000	1	309.0	1854.00	1854	SKK400
	φ800×12	3500	1	233.0	815.50	815	"
	φ800×9	2000	1	176.0	352.00	352	"
	"	12000	1	"	2112.00	2112	"
補強リブ	R-300×9	2542	1	—	53.88	53.9	SS400
ずれ止め	R-25×12	2340	2	—	5.51	11.0	"
吊り金具	R-100×16	120	4	—	1.51	6.0	"
裏当てリング	R-50×4.5	2443	1	—	4.31	4.3	"
ストッパー	R-30×6	30	6	—	0.04	0.2	"
鋼管 φ800 5133 × 40 = 205320 kg							
型鋼 PL 75 × 40 = 3000 "							
合計 5208 × 40 = 208320 kg							
K 1	D29	2420	20	5.04	12.20	244	SD345
2	D13	2440	10	0.995	2.43	24	"
3	"	2180	4	"	2.17	9	"
鉄筋 (SD345) D29 244 × 40 = 9760 kg							
D13 33 × 40 = 1320 "							
合計 277 × 40 = 11080 kg							
中詰めコンクリート (σc k=24N/mm ²) 0.52 × 40 = 20.8 m ³							


現場継手詳細図 S=1:2

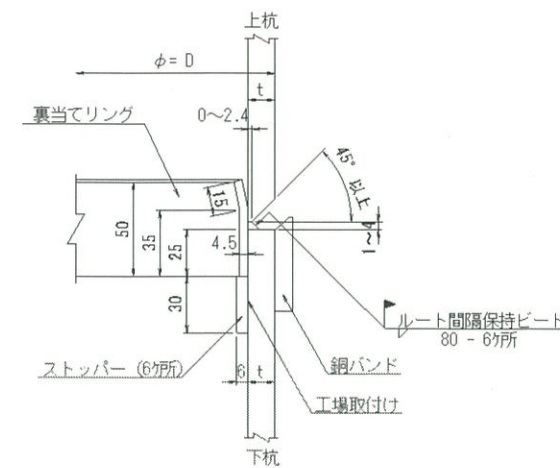


杭先端補強リング詳細図

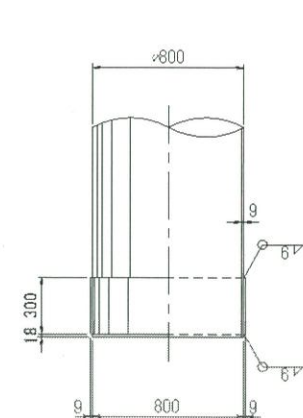

フレアー溶接詳細図

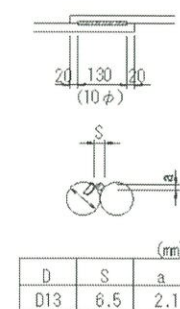

吊金具詳細図 S=1:5

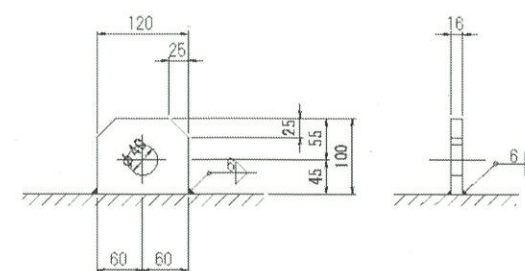

杭配置図

