
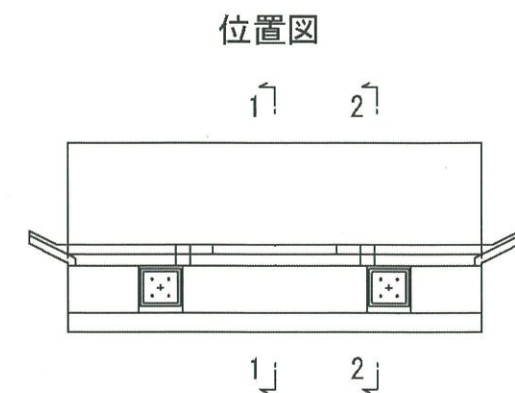
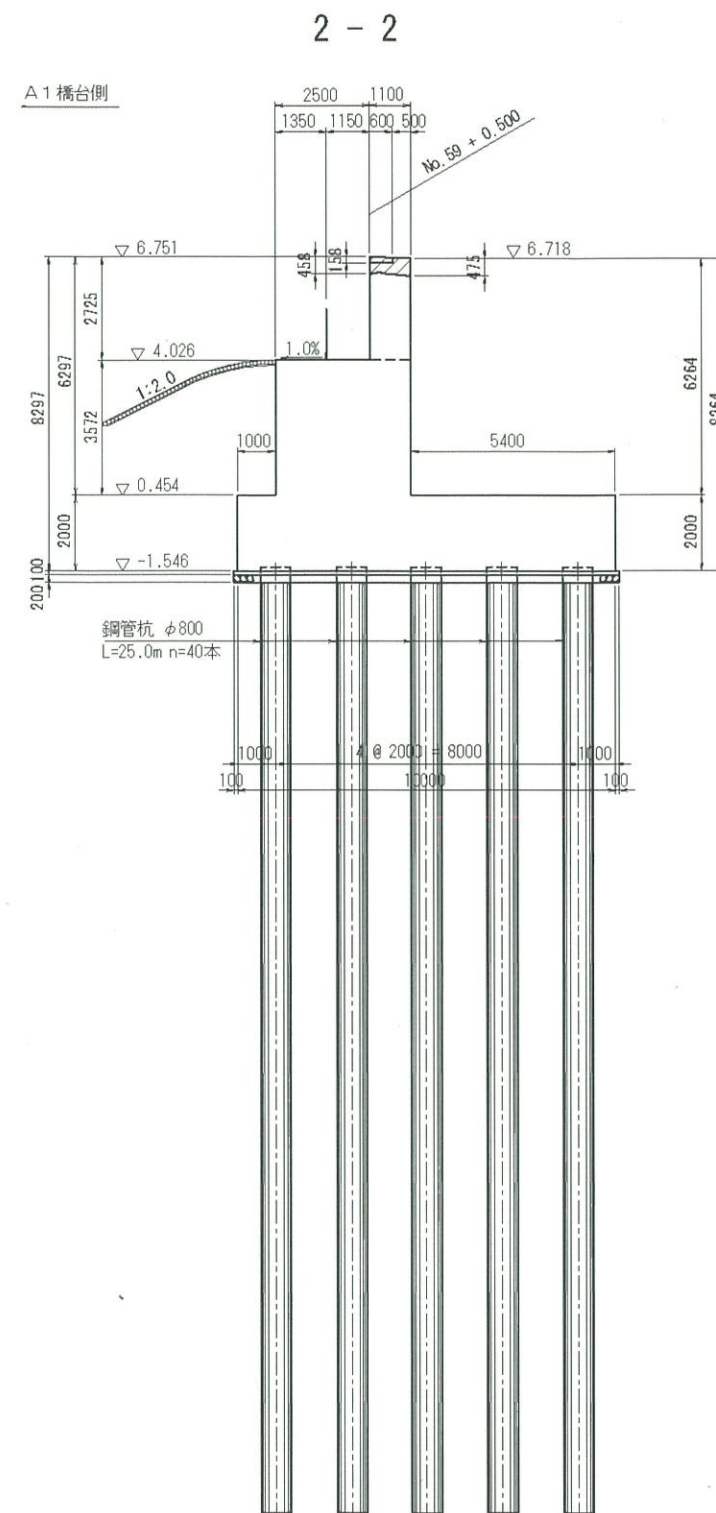


A 2 橋台構造一般図(その2) S=1:100

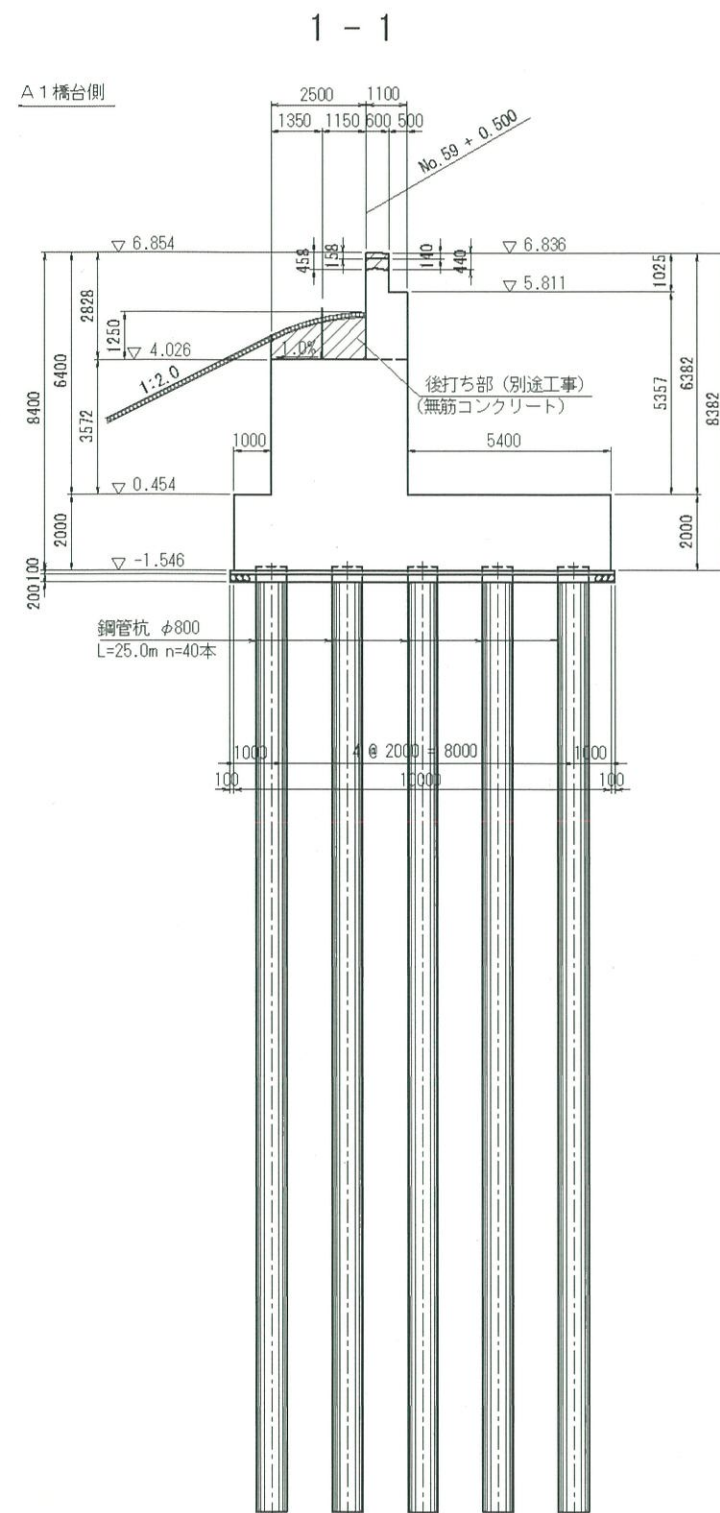

/// 部は、後打ち部 (別途工事) を示す。